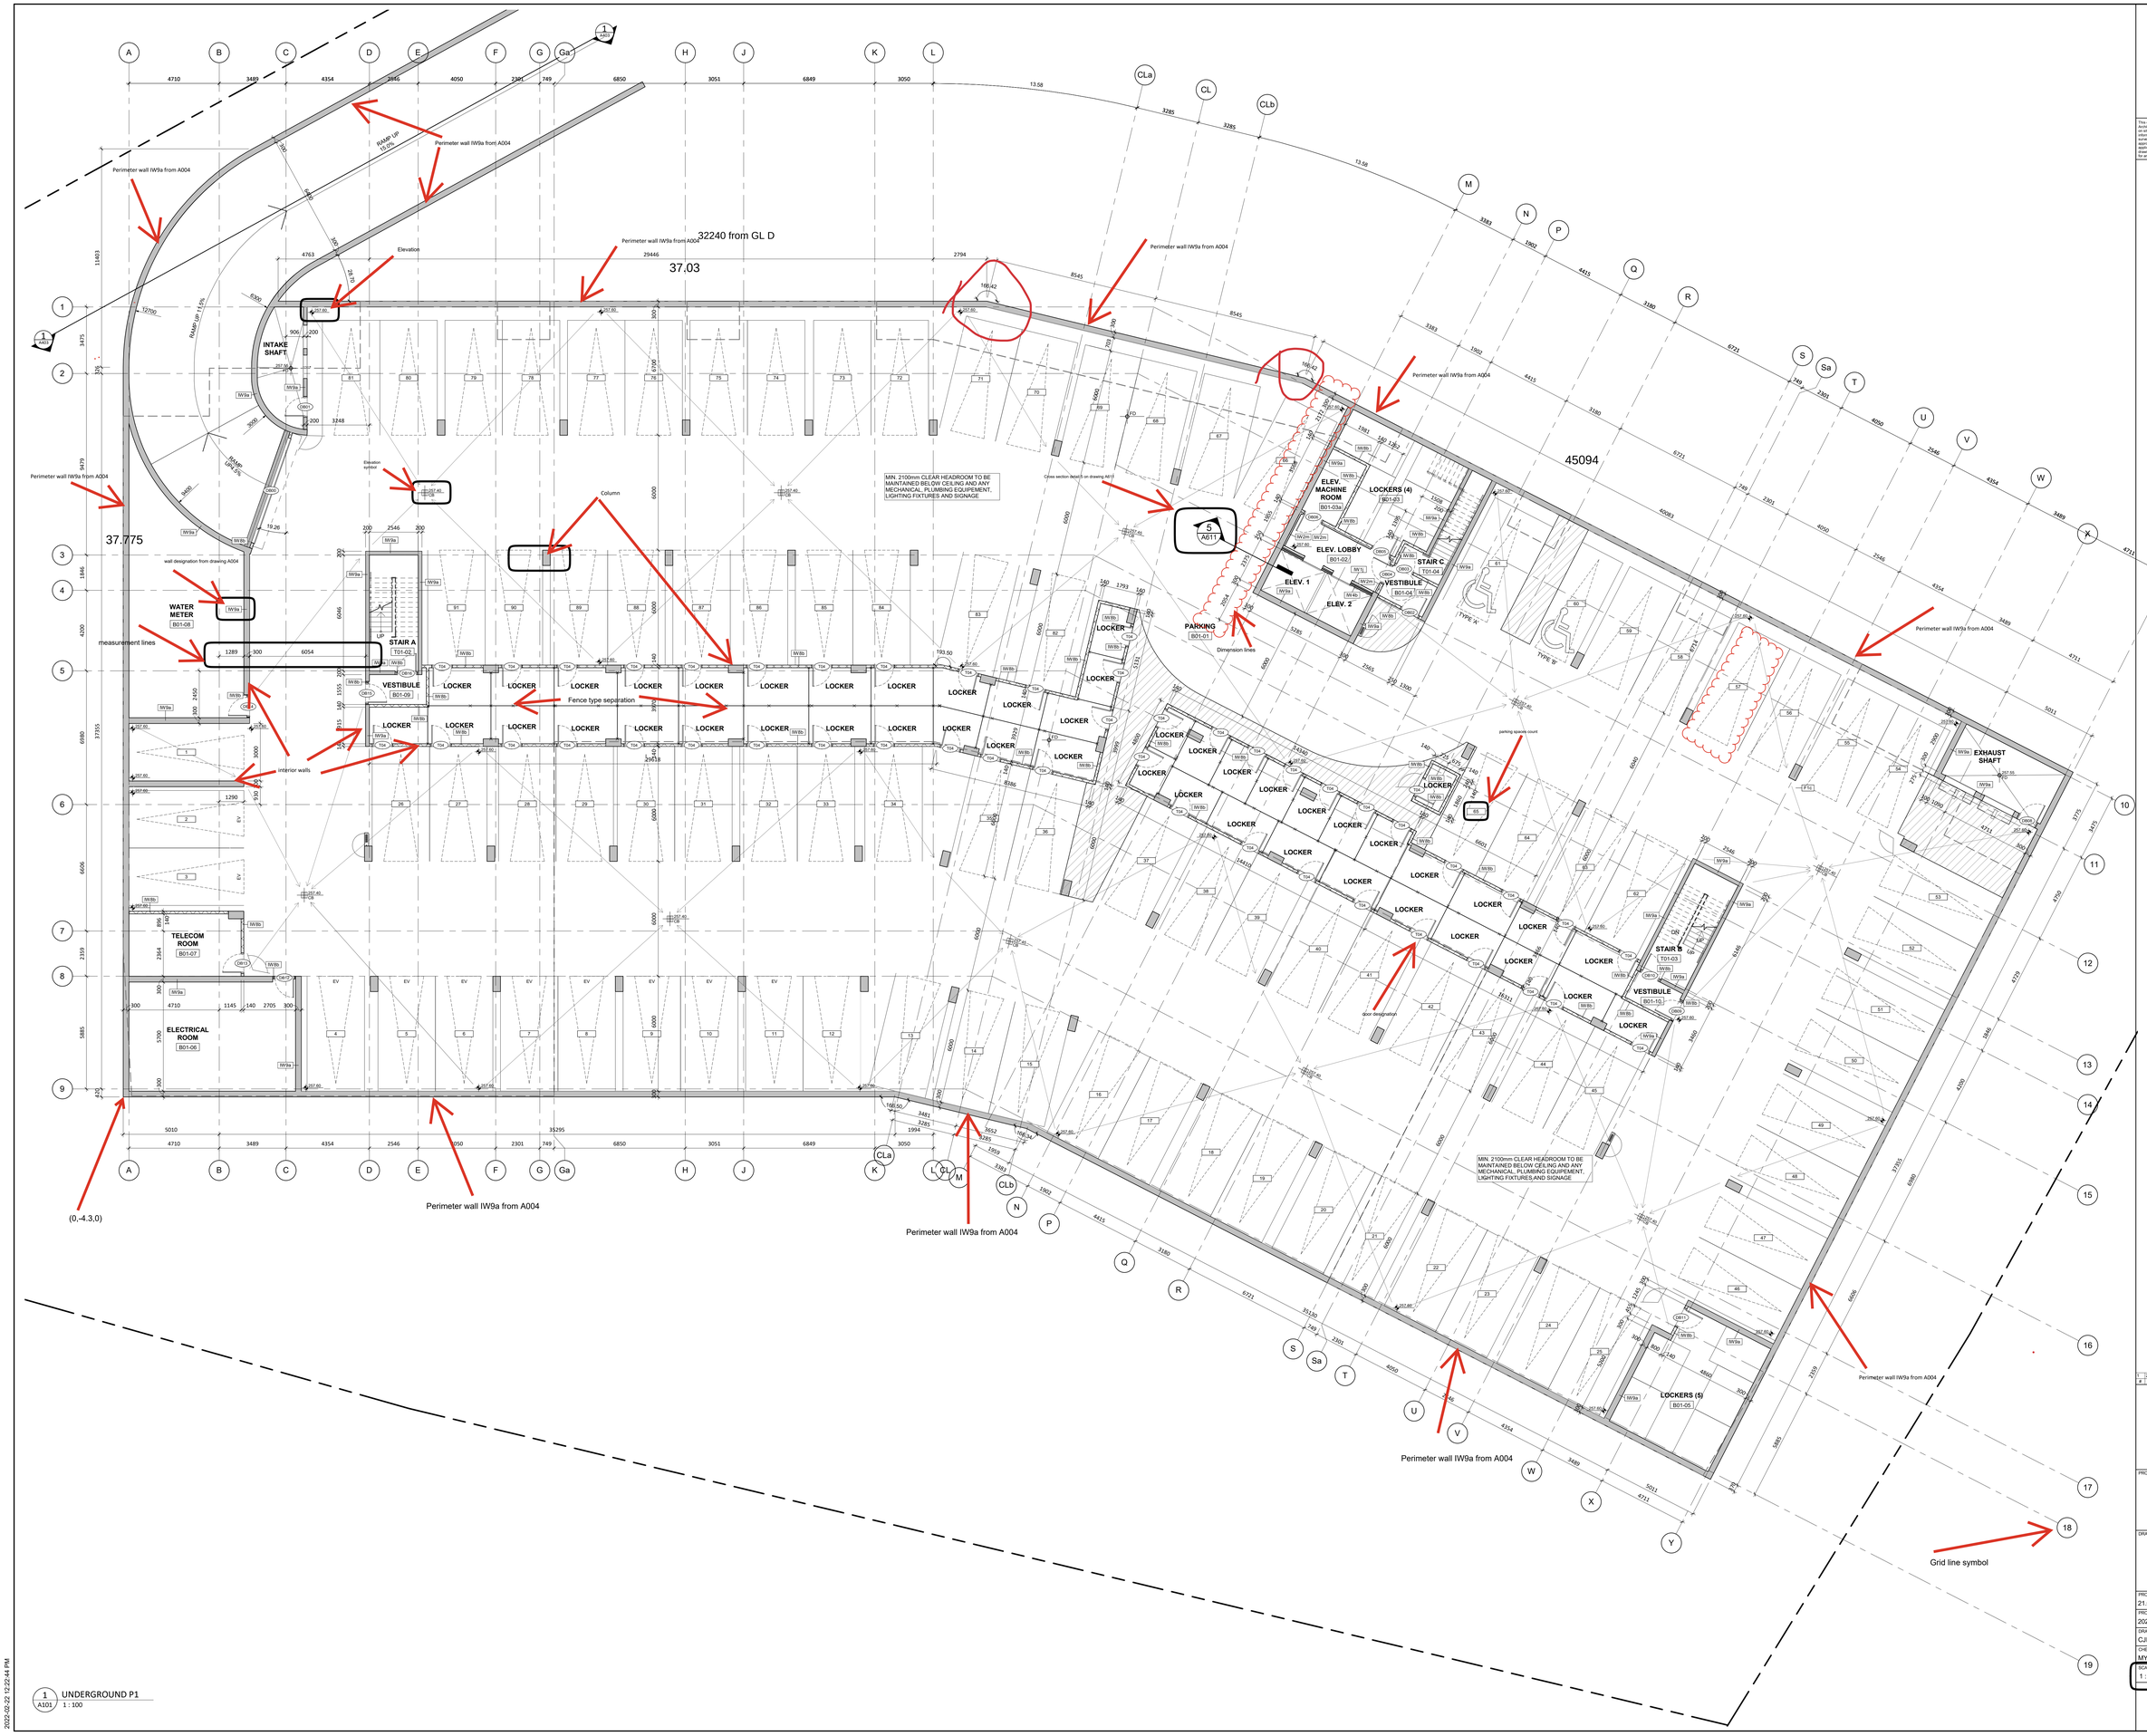

1 A101 UNDERGROUND P1
1 : 100

2022-02-22 12:22:44 PM

This drawing, as an instrument of service, is provided by and is the property of Turner Fleischer Architects Inc. The contractor shall verify and take responsibility for all dimensions and conditions on site and must notify Turner Fleischer Architects Inc. of any variations from the supplied information. This drawing is not to be scaled. The architect is not responsible for the accuracy of CAD files prepared by other consultants. The contractor is responsible for coordinating the work of appropriate consultant's drawings before proceeding with the work. Construction must conform to all applicable codes and requirements of authorities having jurisdiction. The contractor working from drawings and specifications issued for building permit must assume full responsibility and bear costs for any corrections or damages resulting from his work.

#	DATE	DESCRIPTION	BY
1	2021-12-20	ISSUED FOR BUILDING PERMIT	CJF

PROJECT

DRAWING

UNDERGROUND PARKING

PROJECT NO. 21.001CS

PROJECT DATE 2021-05-01

DRAWN BY CJF

CHECKED BY MY

SCALE 1 : 100

DRAWING NO. A101

REV. 1