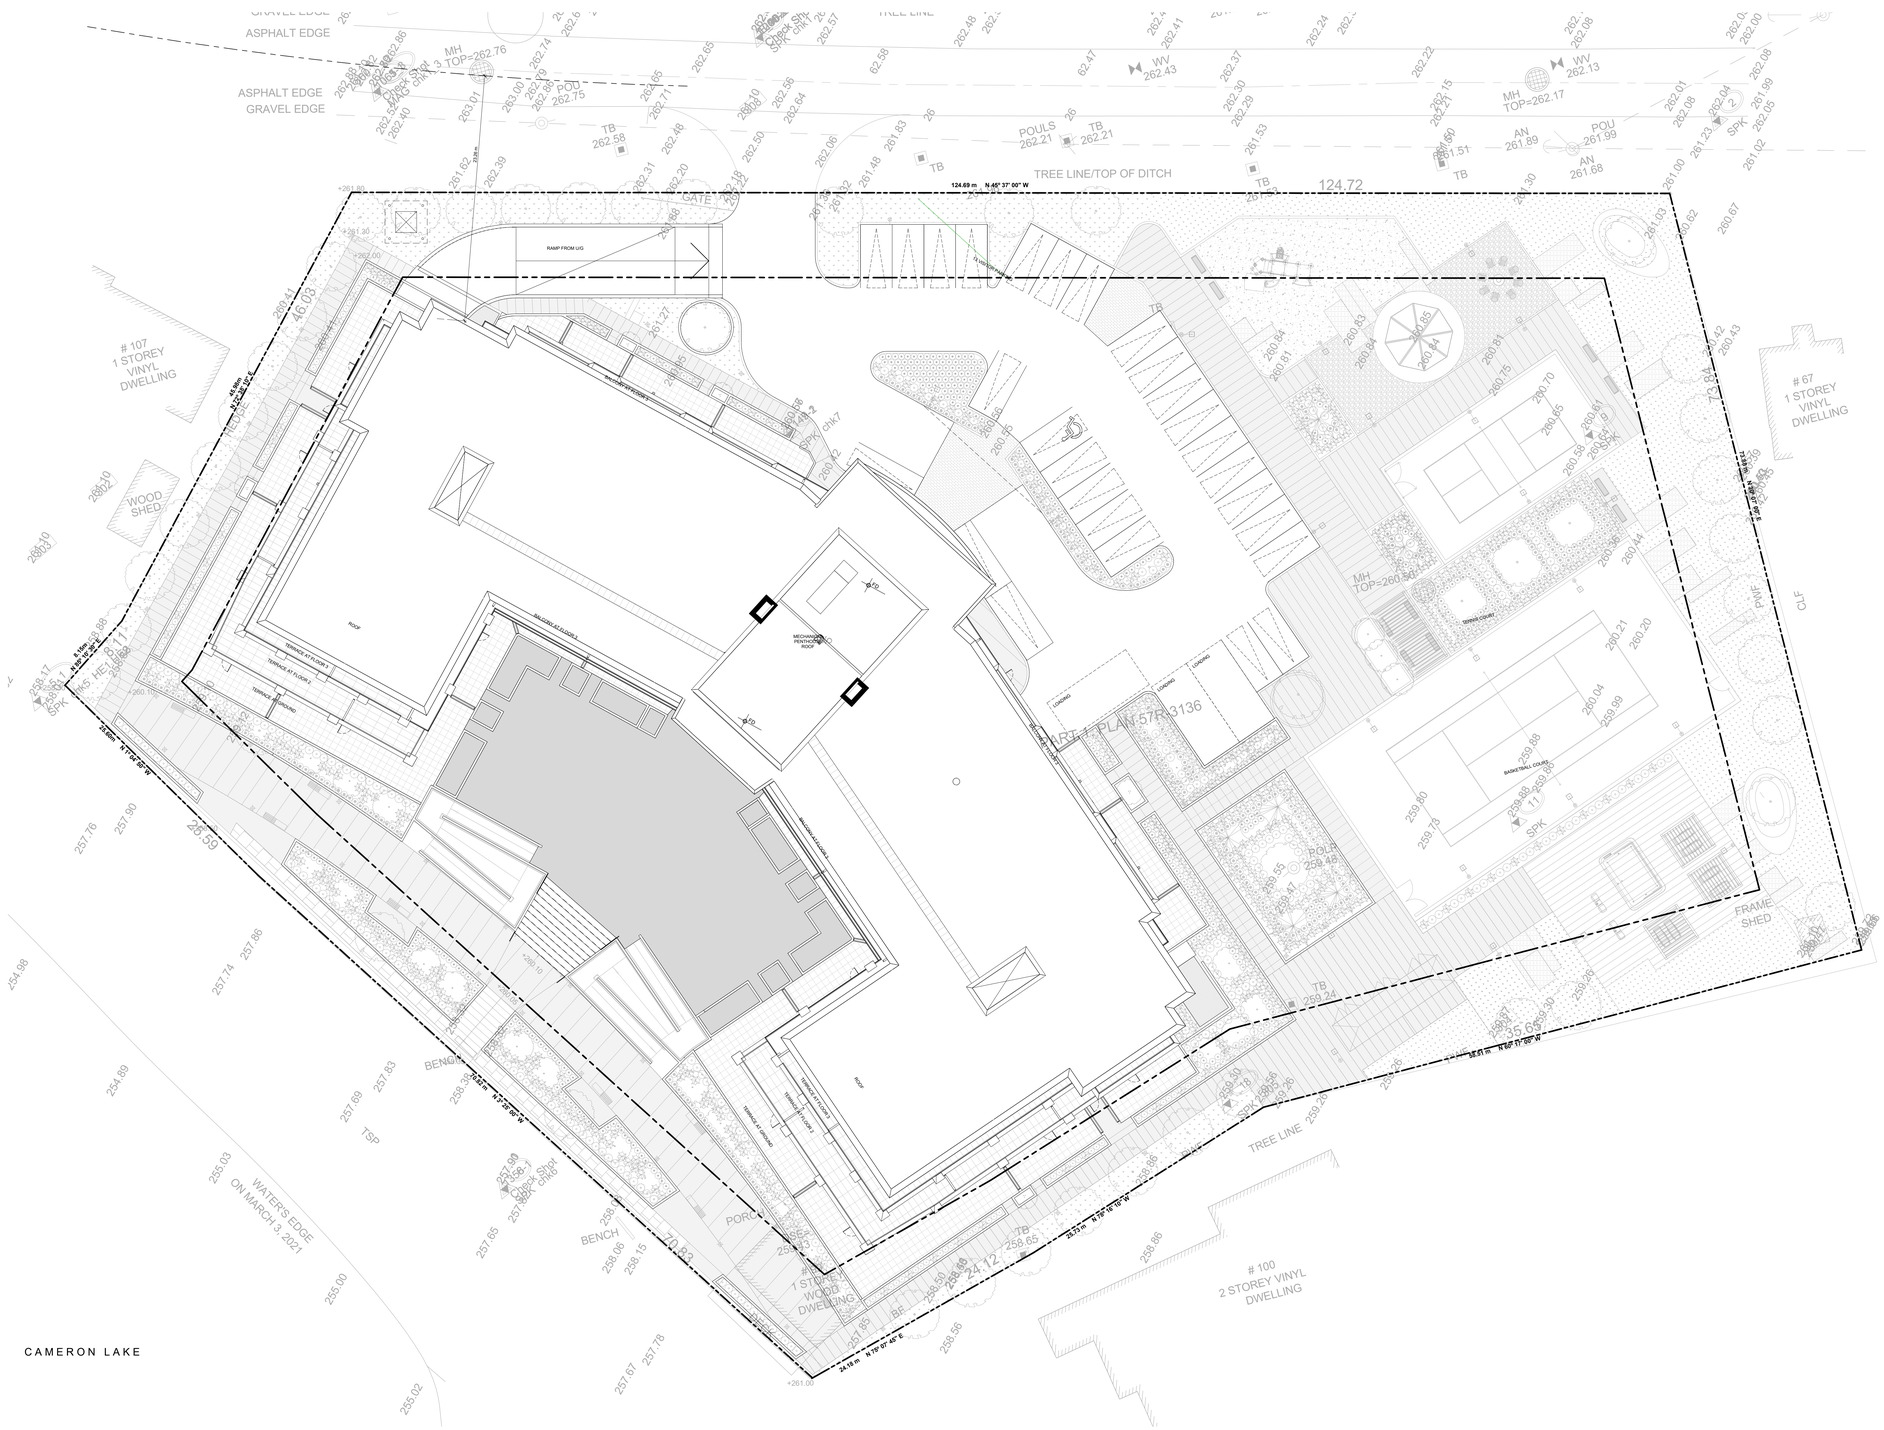

1 SITE PLAN
A002 1 : 200

Item	2012 Ontario Building Code Data Matrix Version: O. Reg. 332/12 Last Amendment: O. Reg. 88/19	OBC Reference
1	Project Description: ☒ New ☐ Part 11 ☐ Addition ☐ Part 3 ☐ Alteration ☐ Change of Use	1.1.2.[A]
2	Major Occupancy(s): **Group C, F3** Subsidiary Occupancy(s): **Group A2**	3.1.2.1.(1)
3	Building Area: (m²) Existing - New **2,962** Total **2,962**	1.4.1.2.[A]
4	Gross Area: (m²) Existing - New **7,929** Total **7,929**	1.4.1.2.[A]
5	Number of Storeys: Above grade: **3** Below grade: **1**	1.4.1.2.[A] & 3.2.1.1.
6	Number of Streets/Access Routes: **1**	3.2.2.10. & 3.2.5.
7	Building Classification: **3.2.2.44 - Group C, up to 4 Storeys, Noncombustible Construction** **3.2.2.77 - Group F, Division 3 up to 4 Storeys, Sprinklered**	3.2.2.44. & 3.2.2.77.
8	Sprinkler System Proposed: ☒ Entire Building ☐ Basement Only ☐ Selected Compartments ☐ In Lieu of Roof Rating ☐ Selected Floor Areas ☐ Not Required	3.2.2.44. & 3.2.2.77. INDEX 3.2.1.5. 3.2.2.17.
9	Standpipe Required: ☒ Yes ☐ No	3.2.9.
10	Fire Alarm Required: ☒ Yes ☐ No	3.2.4.
11	Water Service/Supply is Adequate: ☒ Yes ☐ No	3.2.5.7.
12	High Building: ☐ Yes ☒ No	3.2.6.
13	Permitted Construction: ☐ Combustible ☐ Non-combustible ☒ Both Actual Construction: ☐ Combustible ☒ Non-combustible ☐ Both	3.2.2.44. & 3.2.2.77.
14	Mezzanine(s) Area: (m²) **None**	3.2.1.1.(3)-(8)
15	Occupant load based on: ☐ m² / person ☒ Design of Building Underground — Occupancy: **Parking (F3)** — Load: **80 persons** 1st Floor — Occupancy: **Residential (C)** — Load: **82 persons** 2nd Floor — Occupancy: **Residential (C)** **Amenity (A2)** — Load: **80 persons** **60 persons (max)** 3rd Floor — Occupancy: **Residential (C)** **Amenity (A2)** — Load: **66 persons** **60 persons (max)**	3.1.17.
16	Barrier-free Design: ☒ Yes ☐ No (Explain)	3.8.
17	Hazardous Substances: ☐ Yes ☒ No	3.3.1.2. & 3.3.1.19.
18	Required Fire Resistance Rating (FRR): Horizontal Assemblies FRR (Hours) — Listed Design No. or Description (SB-2) Floors 1 Hours — Poured Concrete min. 90mm Roof 1 Hour — Poured Concrete min. 90mm Mezzanine 1 Hours — Poured Concrete min. 90mm FRR of Supporting Members — Listed Design No. Or Description (SB-2) Floors 1 Hours — Poured Concrete min. 90mm Roof 1 Hour — Poured Concrete min. 90mm Mezzanine 1 Hours — Poured Concrete min. 90mm	3.2.2.20. - 3.2.2.83. & 3.2.1.4
19	Spatial Separation: Wall — L.D. — Permitted Max % Openings — Required FRR (h) — Required Construction Type North — 8.0m — 100%* — none — Both South — 8.0m — 100%* — none — Both East — 12.0m — 100% — none — Both West — 23.26m (C/L of street) — 100% — none — Both *Fire compartments have less than 65m² exposed building face area	3.2.3.

SHEET NUMBER	SHEET NAME
A000	COVER SHEET
A001	SURVEY
A002	SITE PLAN / STATISTICS
A003	FIRE SEPARATION DIAGRAMS
A004	CONSTRUCTION ASSEMBLIES
A101	UNDERGROUND PARKING
A102	GROUND FLOOR PLAN
A103	SECOND FLOOR PLAN
A104	THIRD FLOOR PLAN
A105	MECHANICAL PENTHOUSE
A106	ROOF PLAN
A201	GROUND FLOOR PLAN - A
A202	GROUND FLOOR PLAN - B
A203	GROUND FLOOR PLAN - C
A204	SECOND FLOOR PLAN - A
A205	SECOND FLOOR PLAN - B
A206	SECOND FLOOR PLAN - C
A207	THIRD FLOOR PLAN - A
A208	THIRD FLOOR PLAN - B
A209	THIRD FLOOR PLAN - C
A210	MECHANICAL PENTHOUSE - A
A211	MECHANICAL PENTHOUSE - B
A212	MECHANICAL PENTHOUSE - C
A213	ROOF FLOOR PLAN - A
A214	ROOF FLOOR PLAN - B
A215	ROOF FLOOR PLAN - C
A216	ENLARGED PLANS
A221	UNDERGROUND CEILING PLAN
A222	GROUND CEILING PLAN
A223	SECOND CEILING PLAN
A224	THIRD CEILING PLAN
A301	ELEVATIONS
A302	ELEVATIONS
A303	ELEVATIONS - COLOURED
A304	ELEVATIONS - COLOURED
A401	BUILDING SECTIONS
A402	BUILDING SECTIONS
A501	STAIR DETAILS
A621	TYPICAL DETAILS
A622	TYPICAL DETAILS
A701	DOOR & ROOM FINISH SCHEDULE

	m2	ft2	%
GROSS SITE AREA	**11,870.0**	**127,769**	
GROSS FLOOR AREA	**7,959.8**	**85,583**	
FLOOR SPACE INDEX	0.67		
BUILDING COVERAGE (GROUND FLOOR)	2,962.3	31,887	25%
LANDSCAPED OPEN SPACE	6,732.7	72,471	57%

ZONING SUMMARY

	REQUIRED	PROVIDED
ZONING	R5-5 (EXISTING)	R5-5 (NO CHANGE)
USE	CONDOMINIUM	CONDOMINIUM
MINIMUM LOT AREA	11,400 m	11,870 m
MINIUM LOT FRONTAGE	30 m	124.69 m
SETBACKS - FRONT YARD	12.0 m	12.4 m
- REAR YARD	12.0 m	12.00 m
- SIDE YARD	8.0 m	8.0, 8.0 m
- STREET CENTERLINE	22.9 m	23.26 m
MAXIMUM LOT COVERAGE	40 %	25%
MINIMUM LANDSCAPE OPEN SPACE	30 %	57%
BUILDING HEIGHT	12 m	12 m
LOADING SPACES	3	3

GROSS FLOOR AREA (GFA) CALCULATIONS

FLOOR	# FLOORS	RES. UNITS / FLOOR	GROSS FLOOR AREA BREAKDOWN: RESIDENTIAL SALEABLE m2	RESIDENTIAL SALEABLE ft2	RESIDENTIAL NON-SALEABLE m2	RESIDENTIAL NON-SALEABLE ft2	TOTAL RESIDENTIAL m2	TOTAL RESIDENTIAL ft2	INDOOR AMENITY m2	INDOOR AMENITY ft2	GROSS FLOOR AREA m2	GROSS FLOOR AREA ft2
LIG P1	-	-			0	21.7	233	21.7	233	0	21.7	233
GROUND	1	19	2,283.2	24,576	672.5	7,239	2,955.7	31,815	6.7	72	2,962.3	31,887
2ND	1	20	2,237.5	24,084	218.4	2,350	2,455.8	26,435	207.6	2,234	2,663.4	28,669
3RD	1	18	1,936.7	20,847	214.8	2,312	2,151.5	23,159	151.9	1,635	2,303.4	24,794
TOTAL	**3**	**57**	**6,457.3**	**69,507**	**1,127.3**	**12,135**	**7,584.7**	**81,645**	**366.2**	**3,941**	**7,950.8**	**85,583**

UNIT SUMMARY

FLOOR	UNIT TYPE 1B	1B+D	2B	2B+D	3B	3B+D	TOTAL
GROUND	0	1	4	10	4	0	19
2ND FLOOR	0	2	9	7	2	0	20
3RD FLOOR	0	3	11	4	0	0	18
SUBTOTAL	0	6	24	21	6	0	57
UNIT MIX	**0.0%**	**10.5%**	**42.1%**	**36.8%**	**10.5%**	**0.0%**	**100%**

GROSS FLOOR AREA DEFINITION

VILLAGE OF FENELON FALLS, COMPREHENSIVE ZONING BY-LAW 89-25

FLOOR AREA, GROSS - shall mean the total floor area, as hereinafter defined, exclusive of any portion of the building or structure below finished grade which is used for heating, the storage of goods or personal effects, laundry facilities, recreational areas, the storage or parking of motor vehicles or quarters used by the caretaker, watchperson or other supervisor of the building or structures; and, in the case of a dwelling house, exclusive of any private garage, carport, basement, cellar, porch or deck, verandah or sunroom unless such sunroom in habitable during all season of the year.

FLOOR AREA, TOTAL - shall mean the aggregate of the horizontal areas of each floor, whether any such floor is above or below grade, measured between the exterior faces of the exterior walls of

VEHICULAR PARKING - REQUIRED

USE	RATIO (MIN.)	SPACES (MIN.)
VISITOR	-	-
RESIDENTS	1.5 / UNIT	86
TOTAL:		**86**

VEHICULAR PARKING - PROVIDED

LEVEL	RES	VISITOR	TOTAL
U/G P1	92	0	92
GROUND	0	13	13
			105

This drawing, as an instrument of service, is provided by and is the property of Turner Fleischer Architects Inc. All rights including copyright are retained by the architect. Contractor shall verify all dimensions on site and must notify Turner Fleischer Architects Inc. of any variations from the supplied information. This drawing is not to be scaled. The architect is not responsible for the accuracy of any data or information provided by others. Shop drawings must be submitted to the architect for the appropriate consultant's drawings before proceeding with the work. Construction must conform to all applicable codes and requirements of authorities having jurisdiction. The contractor working from drawings prepared by Turner Fleischer Architects Inc. assumes full responsibility and bear costs for any corrections or damages resulting from his work.

#	DATE	DESCRIPTION	BY
1	2021-12-20	ISSUED FOR BUILDING PERMIT	CJF

PROJECT

DRAWING
SITE PLAN / STATISTICS

PROJECT NO. 21.001CS
PROJECT DATE 2021-05-01
DRAWN BY CJF
CHECKED BY MY
SCALE As indicated

DRAWING NO. A002
REV 1

2022-02-22 12:22:23 PM