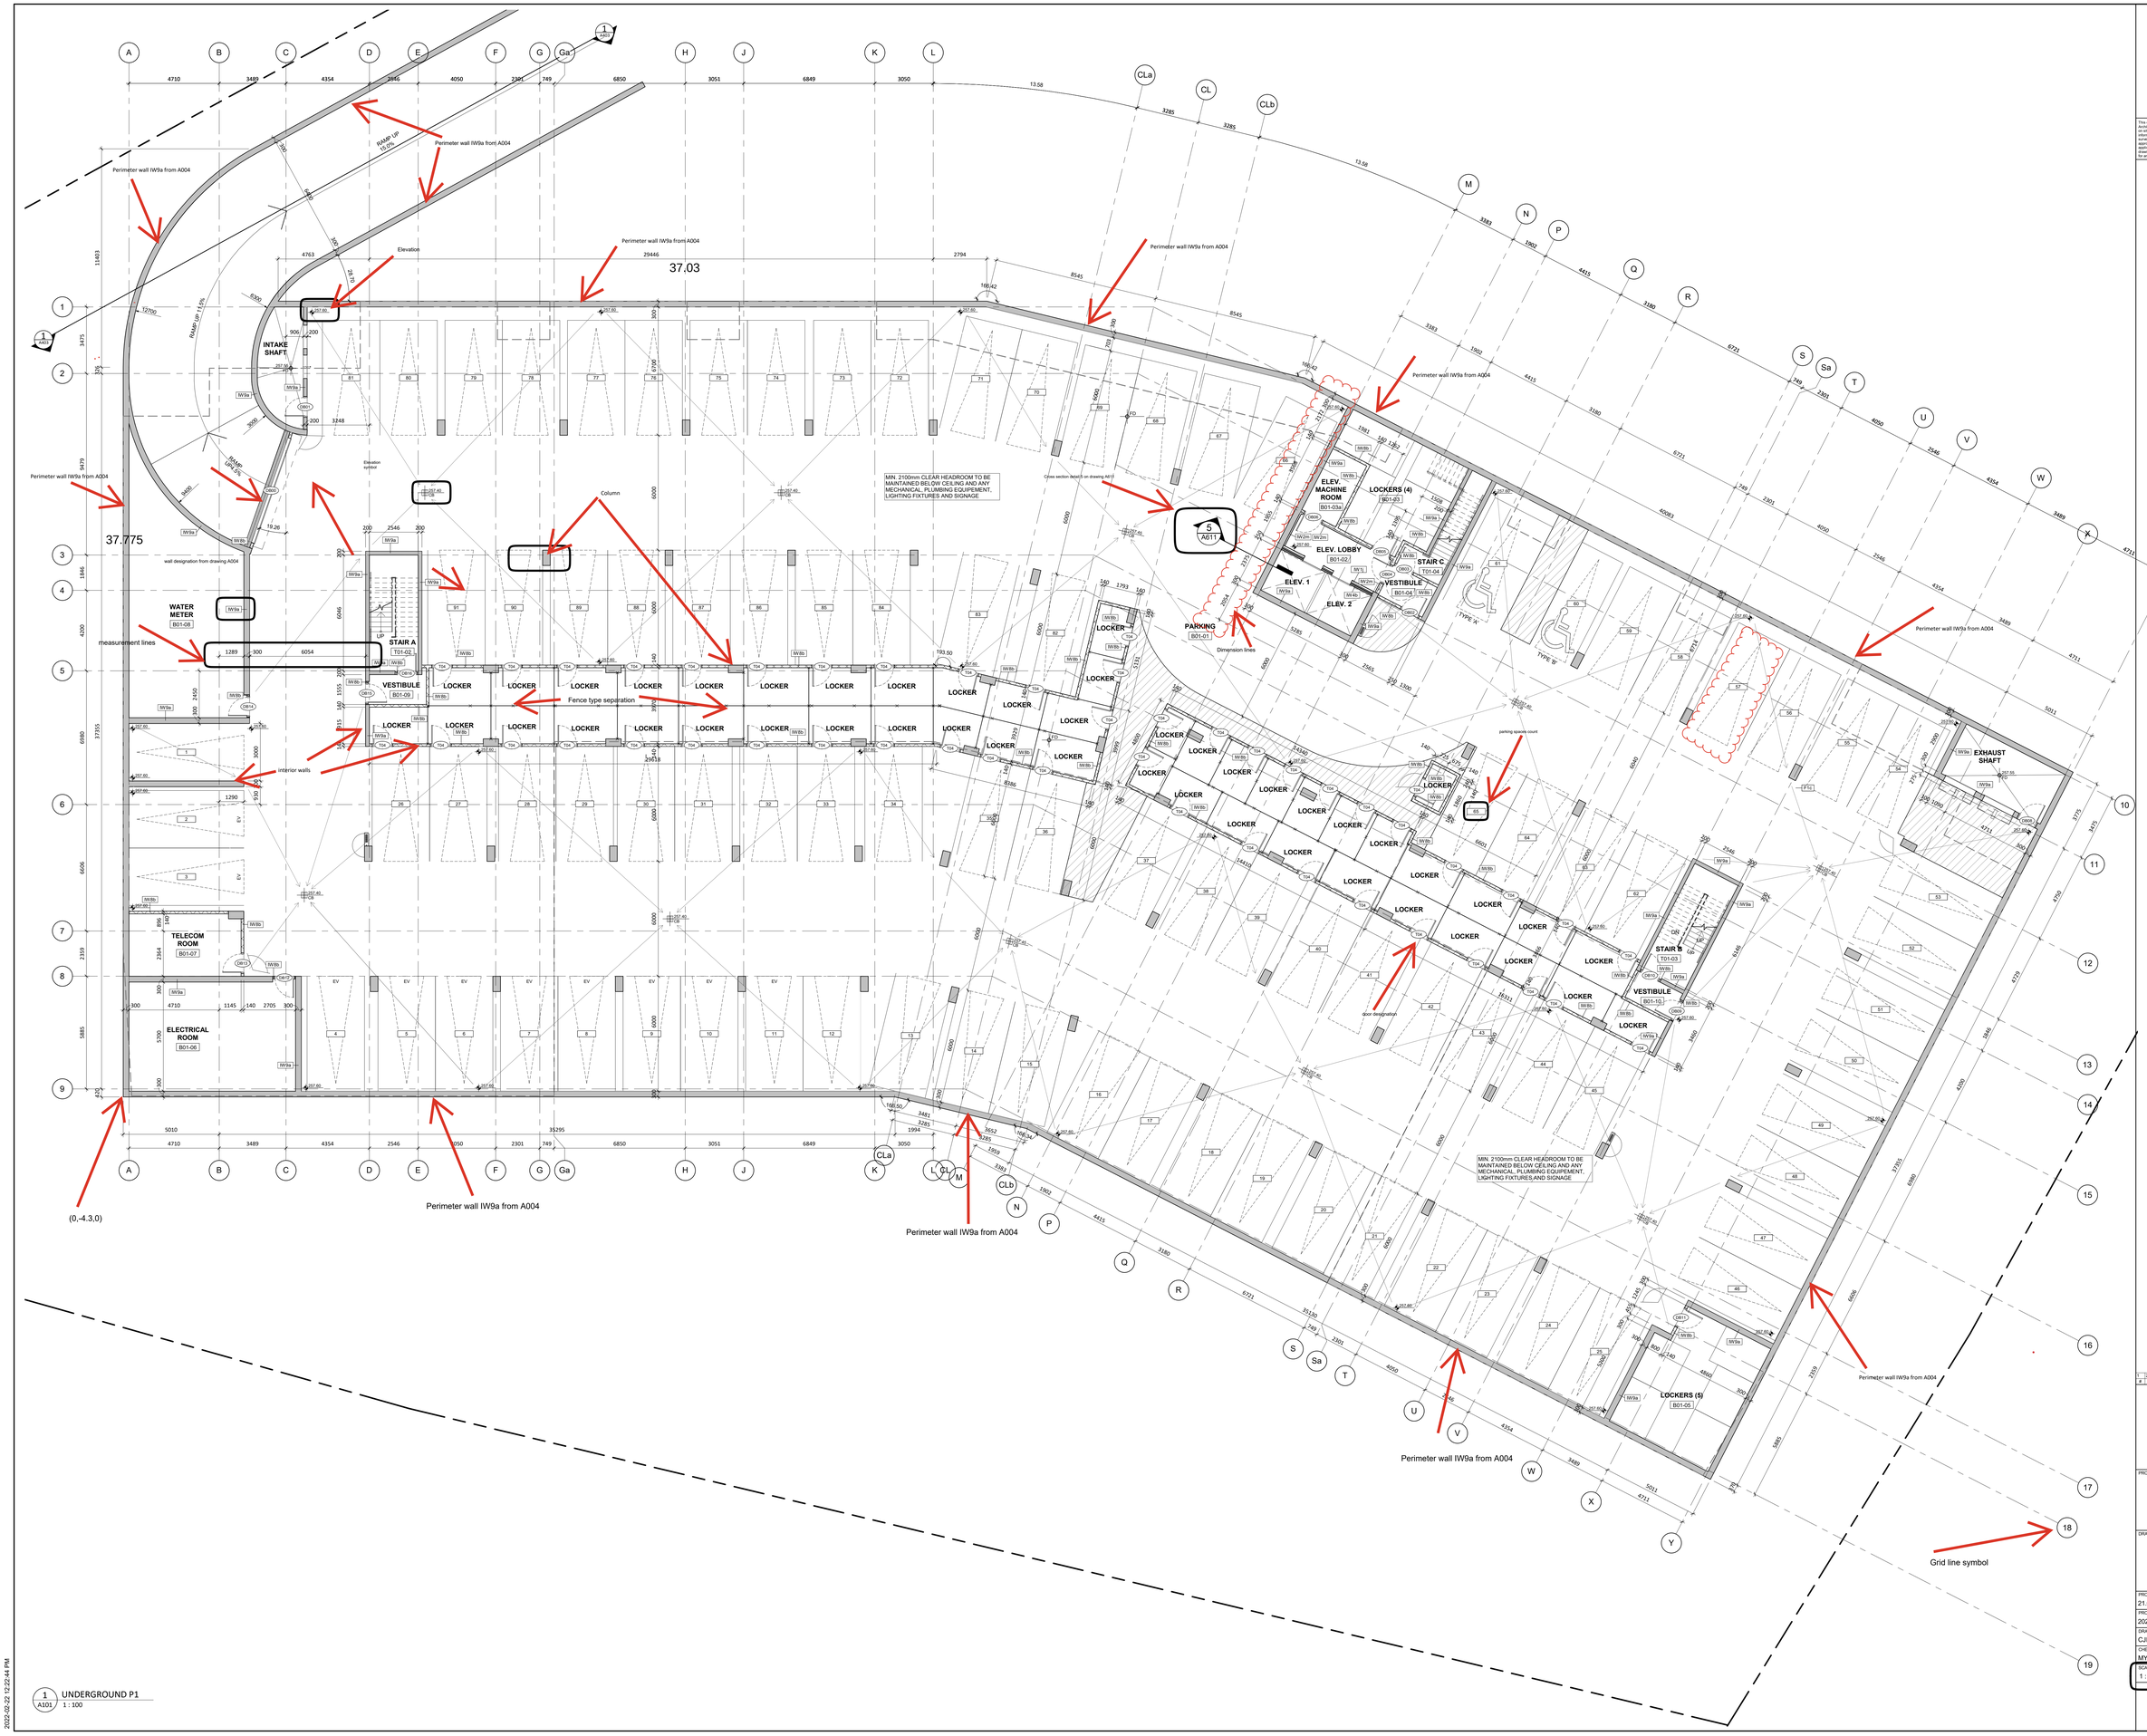


1 A101 UNDERGROUND P1
1 : 100

2022-02-22 12:22:44 PM

This drawing, as an instrument of service, is provided by and is the property of Turner Fleischer Architects Inc. and may not be altered or reproduced without the permission of Turner Fleischer Architects Inc. Contractors shall verify and take responsibility for all dimensions on site and must notify Turner Fleischer Architects Inc. of any variations from the supplied information. This drawing is not to be scaled. The architect is not responsible for the accuracy of CAD files prepared by other consultants. Contractors are responsible for coordinating their work with all other consultant's drawings before proceeding with the work. Construction must conform to all applicable codes and requirements of authorities having jurisdiction. The contractor working from drawings and specifications issued for "Building Permit" must assume full responsibility and bear costs for any corrections or damages resulting from his work.

| # | DATE | DESCRIPTION | BY |
|---|---|---|---|
| 1 | 2021-12-20 | ISSUED FOR BUILDING PERMIT | CJF |

PROJECT

DRAWING
**UNDERGROUND PARKING**

PROJECT NO. 21.001CS
PROJECT DATE 2021-05-01
DRAWN BY CJF
CHECKED BY MY
SCALE 1 : 100
DRAWING NO. A101
REV. 1