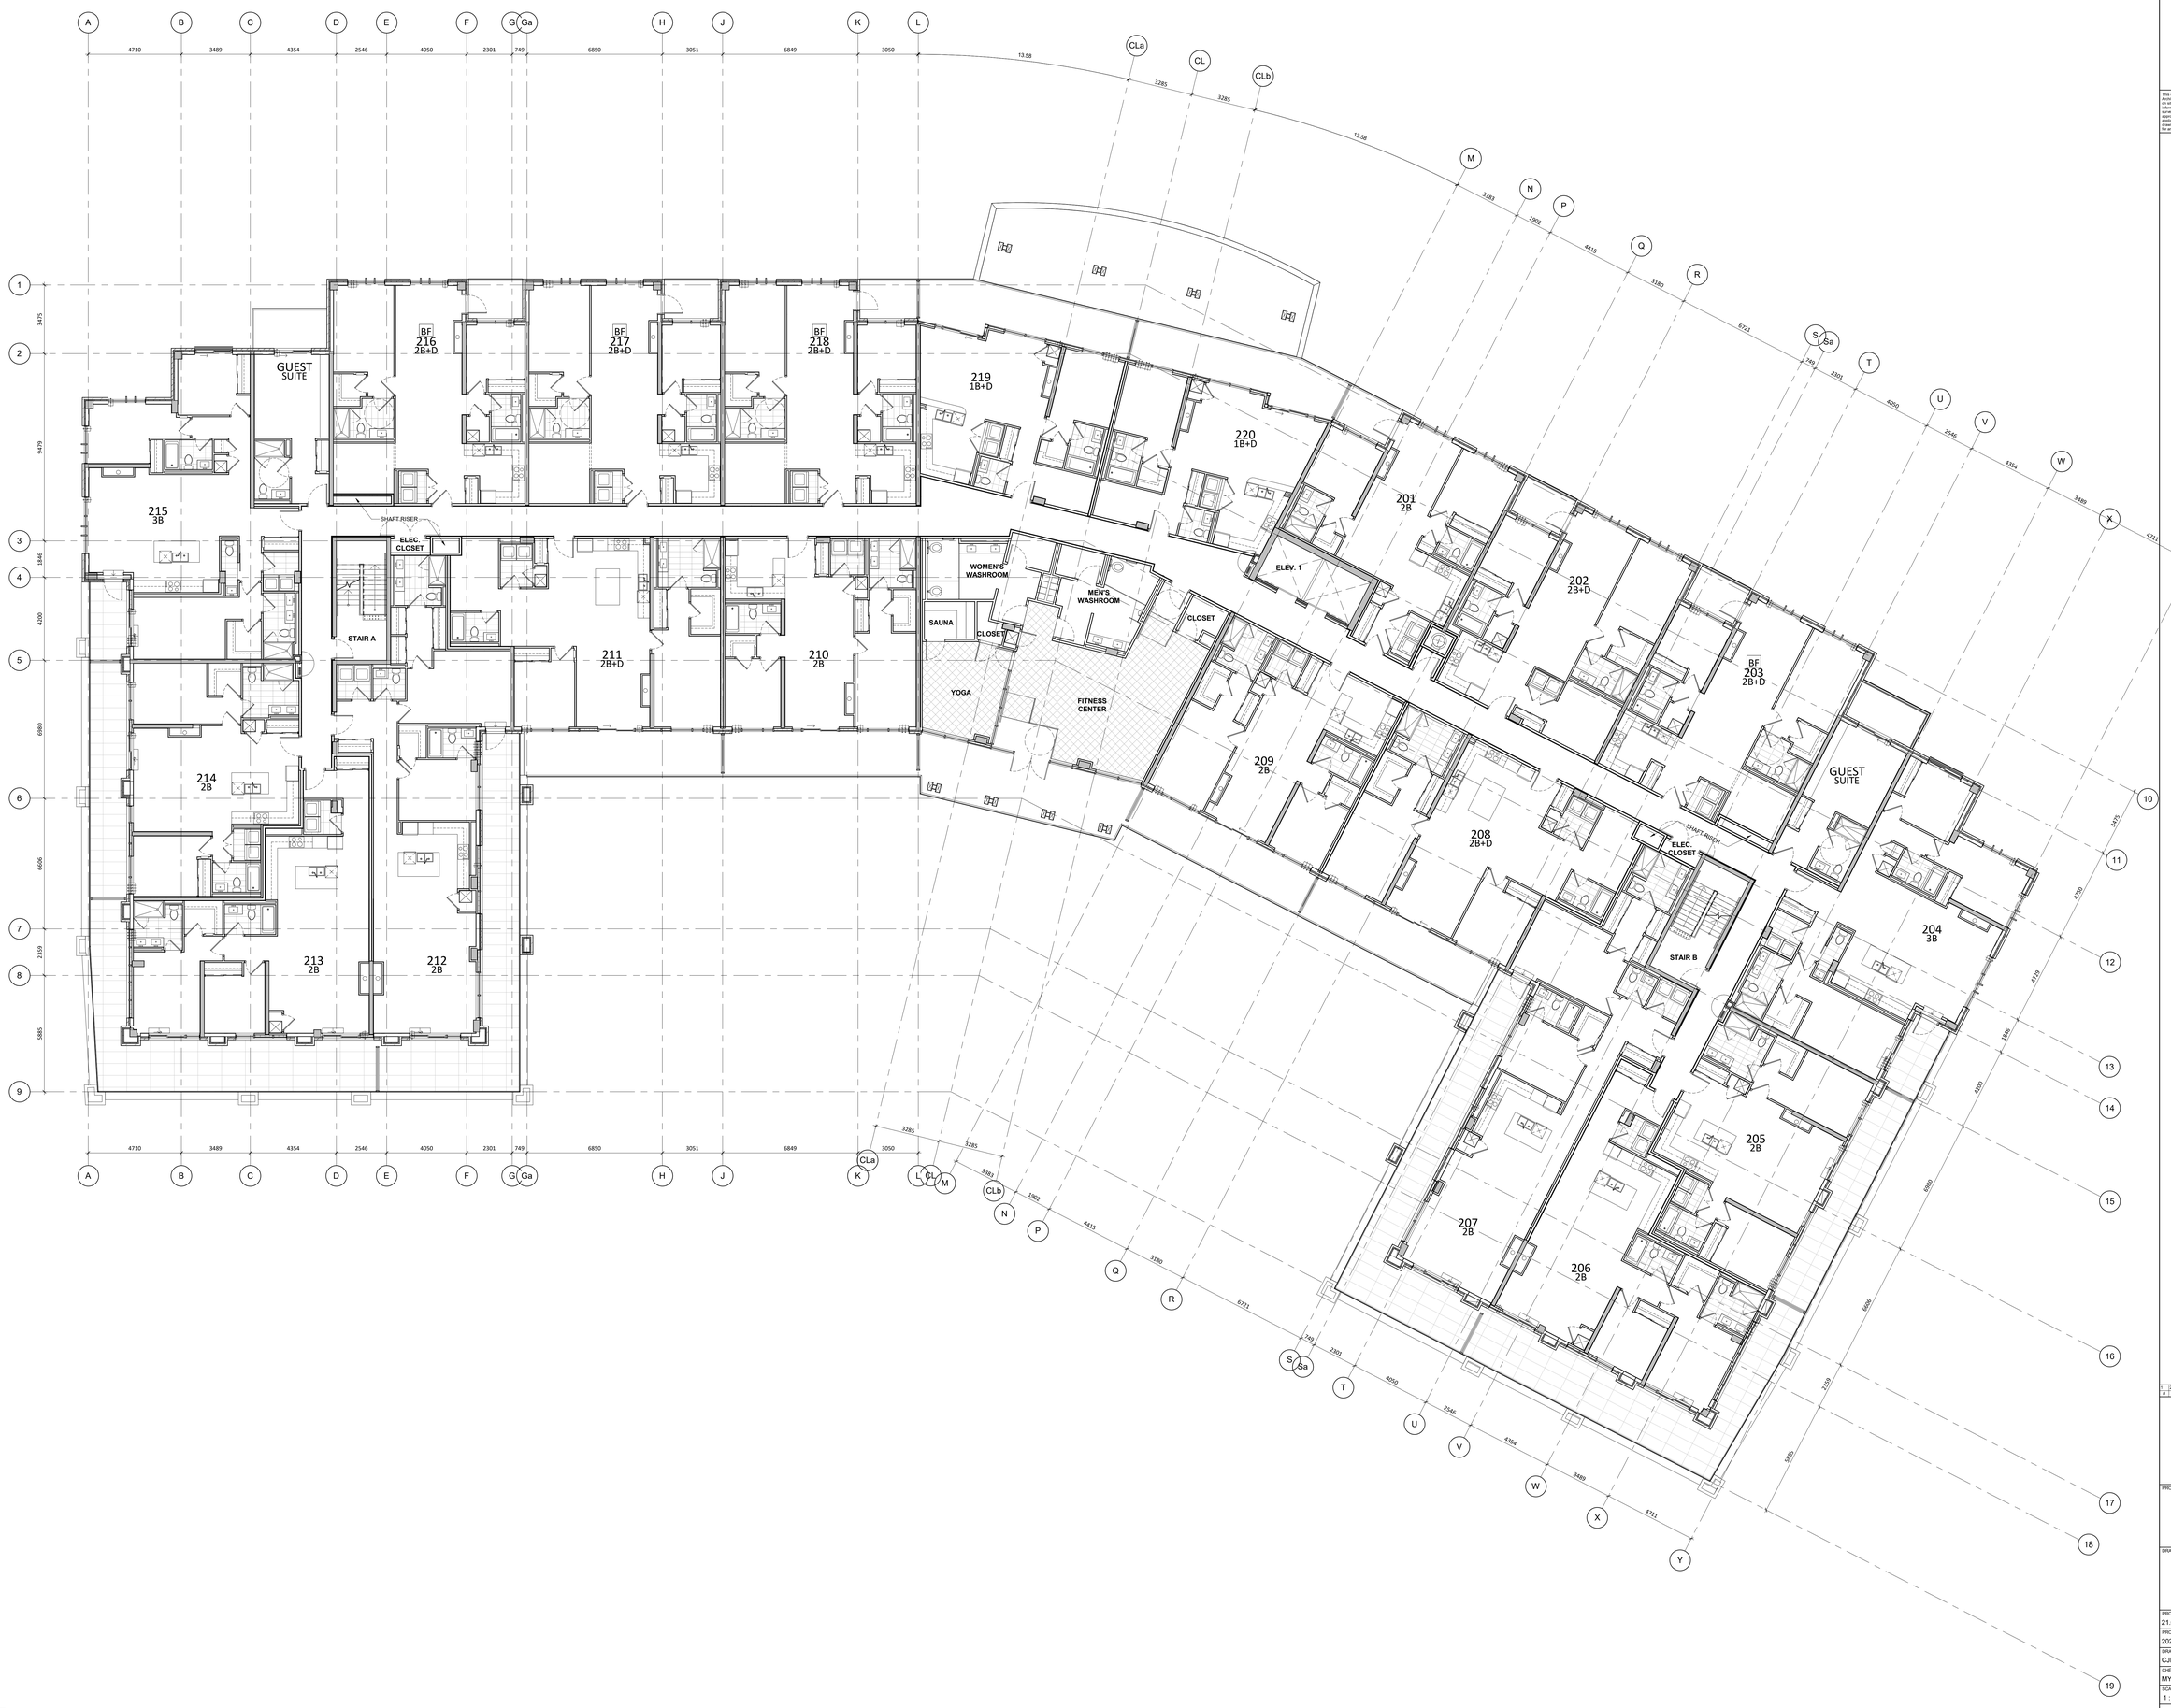

1 FLOOR 2
A103 1 : 100

2022-02-22 12:23:01 PM

This drawing, as an instrument of service, is provided by and is the property of Turner Fleischer Architects Inc. and may be used only for the purpose agreed to by Turner Fleischer Architects Inc. Contractors shall verify and take responsibility for all dimensions and conditions on site and must notify Turner Fleischer Architects Inc. of any variations from the supplied information. This drawing is not to be scaled. The architect is not responsible for the accuracy of copies made by others from electronic files. Construction must comply with the National Building Code and all applicable consultant's drawings before proceeding with the work. Construction must conform to all applicable codes and requirements of authorities having jurisdiction. The contractor working from drawings and specifications issued for construction is deemed to and assume full responsibility and bear costs for any corrections or damages resulting from his work.

#	DATE	DESCRIPTION	BY
1	2021-12-20	ISSUED FOR BUILDING PERMIT	CJF

PROJECT

DRAWING

SECOND FLOOR PLAN

PROJECT NO	21.001CS
PROJECT DATE	2021-05-01
DRAWN BY	CJF
CHECKED BY	MY
SCALE	1 : 100
DRAWING NO	A103
REV	1