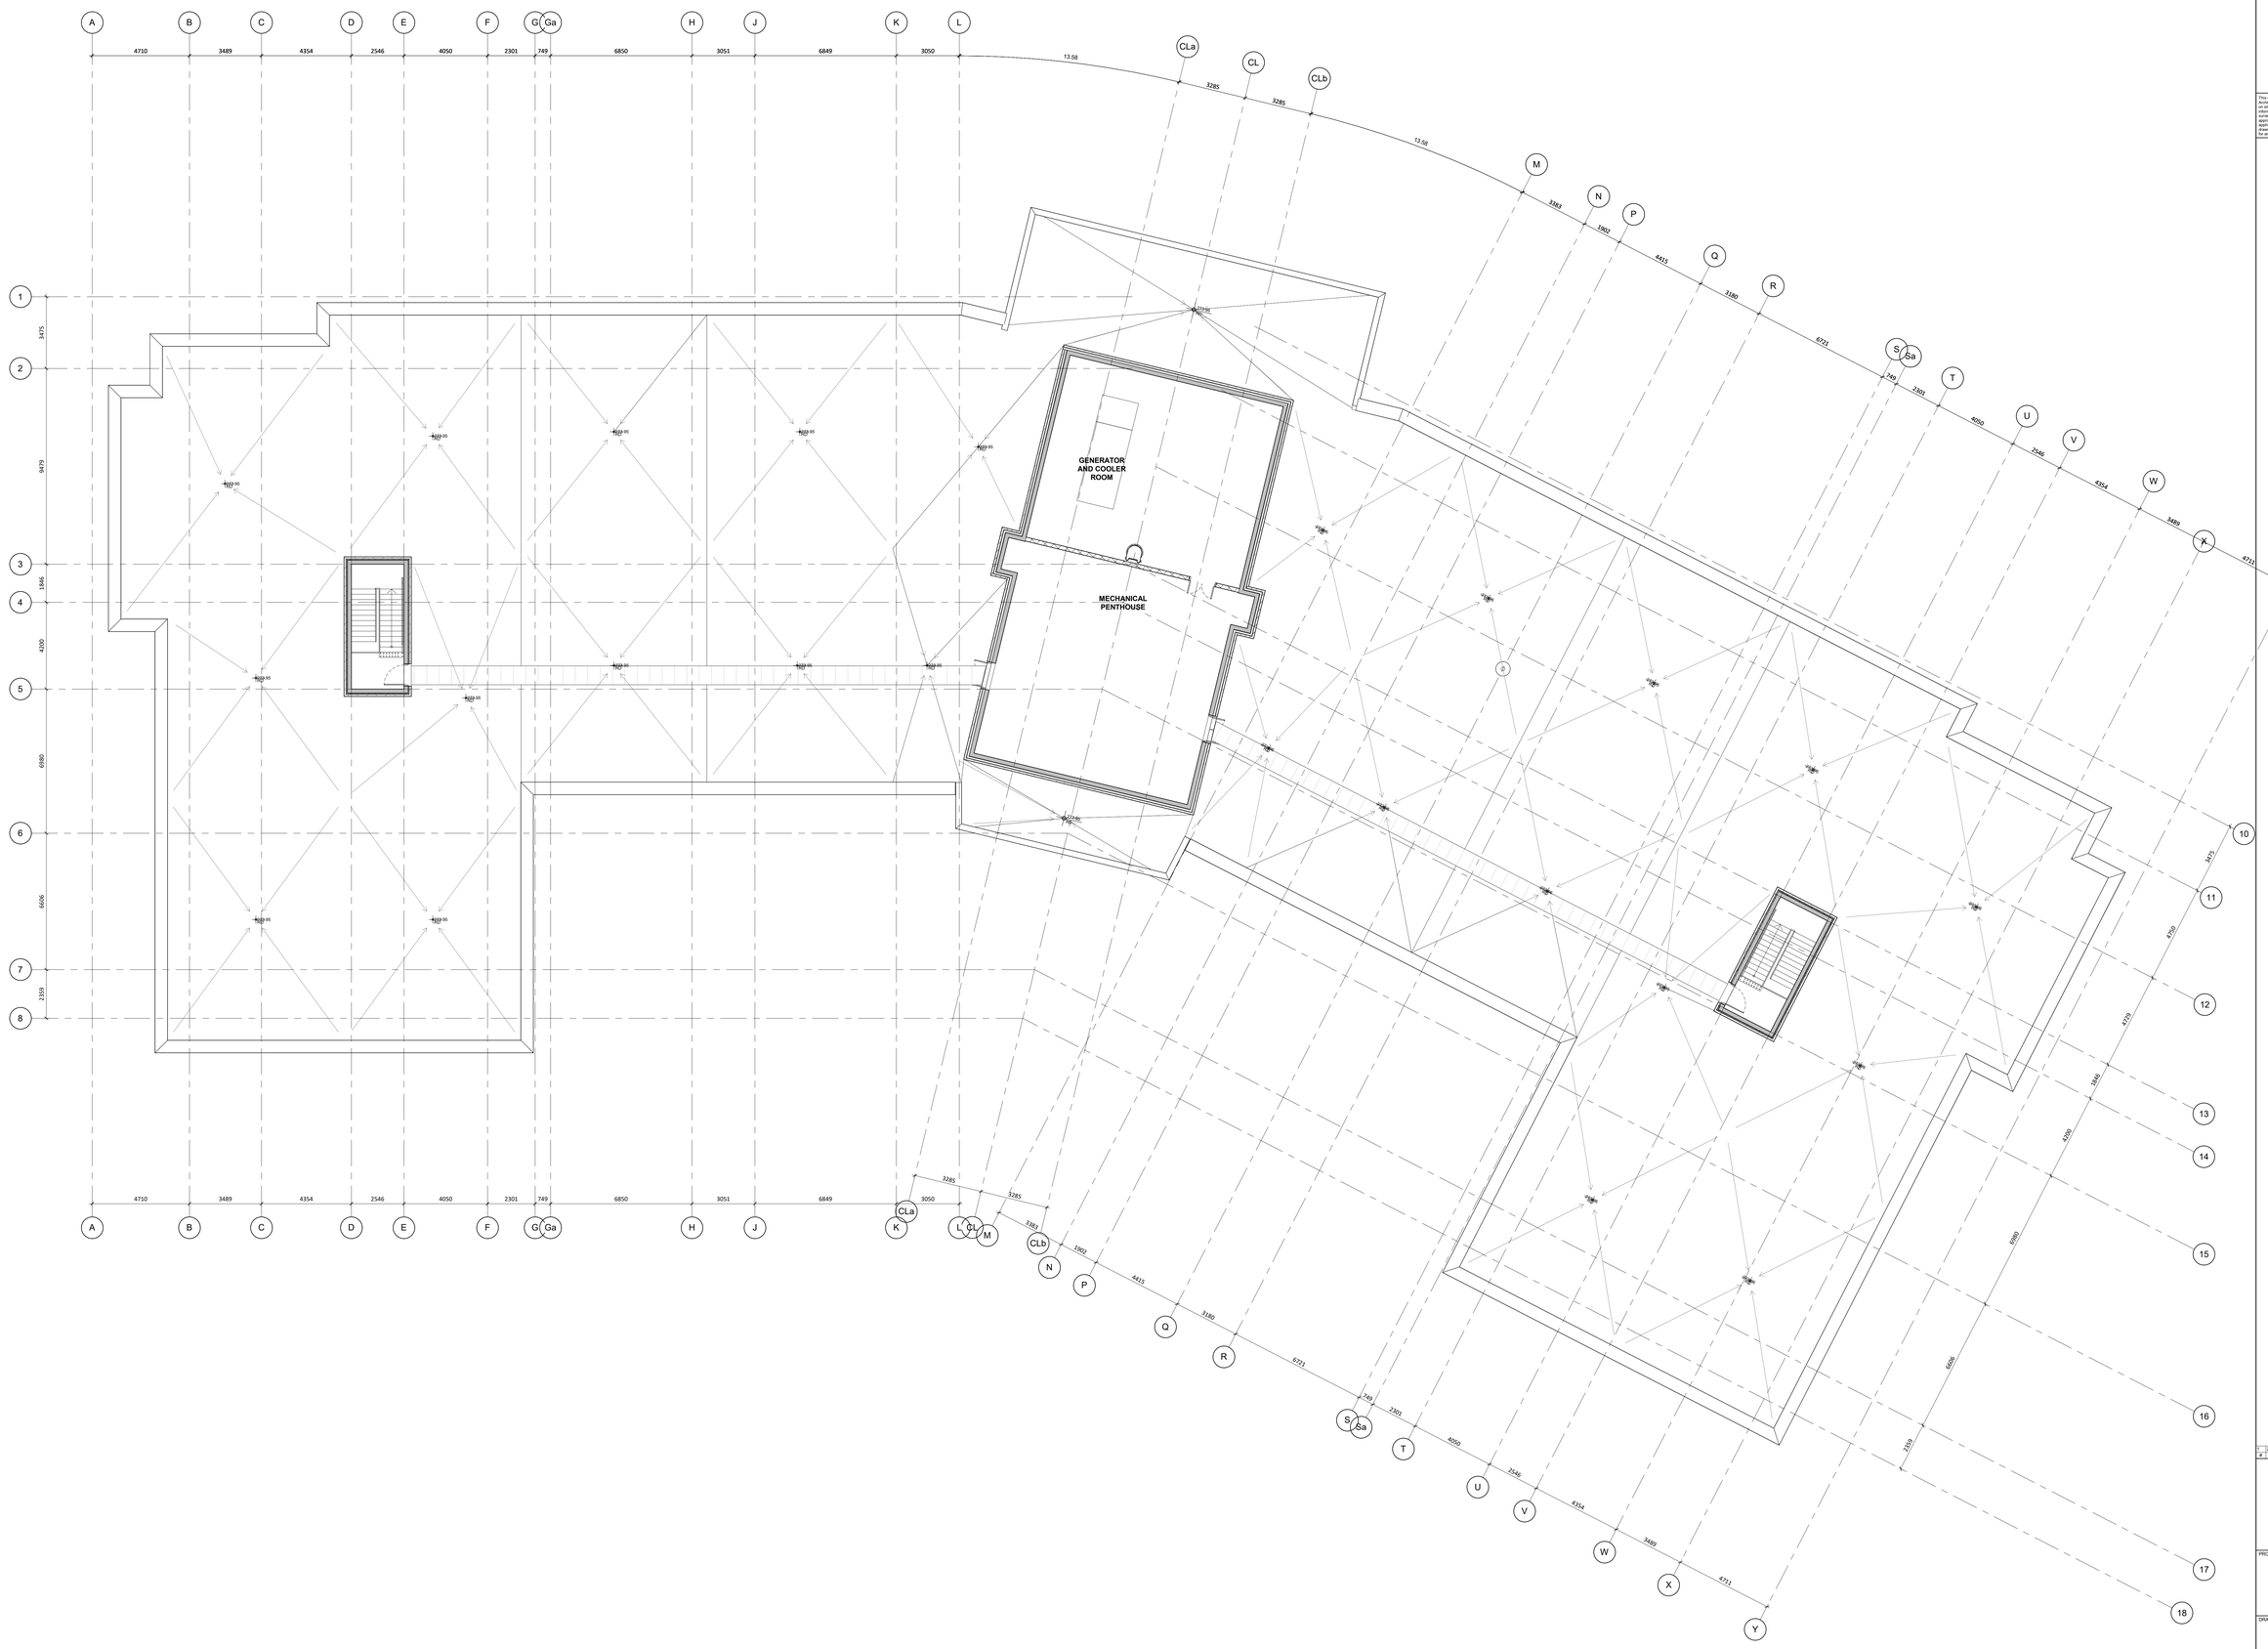

1 A105 MECHANICAL PENTHOUSE
1 : 100

This drawing, as an instrument of service, is provided by and is the property of Turner Fleischer Architects Inc. and may not be altered without the consent of Turner Fleischer Architects Inc. Contractor shall verify and take responsibility for all dimensions on site and must notify Turner Fleischer Architects Inc. of any variations from the supplied information. This drawing is not to be scaled. The architect is not responsible for the accuracy of CAD files prepared by other consultants. Contractor shall coordinate all work with the work of all other consultants and shall review all shop drawings prior to commencement of any work. Construction must conform to all applicable codes and requirements of authorities having jurisdiction. The contractor working from drawings and specifications issued for construction is deemed to accept and assume full responsibility and bear costs for any corrections or damages resulting from his work.

#	DATE	DESCRIPTION	BY
1	2021-12-20	ISSUED FOR BUILDING PERMIT	CJF

PROJECT

DRAWING

MECHANICAL PENTHOUSE

PROJECT NO. 21.001CS
PROJECT DATE 2021-05-01
DRAWN BY CJF
CHECKED BY MY
SCALE 1 : 100

DRAWING NO. A105
REV 1

2022-02-22 12:23:10 PM