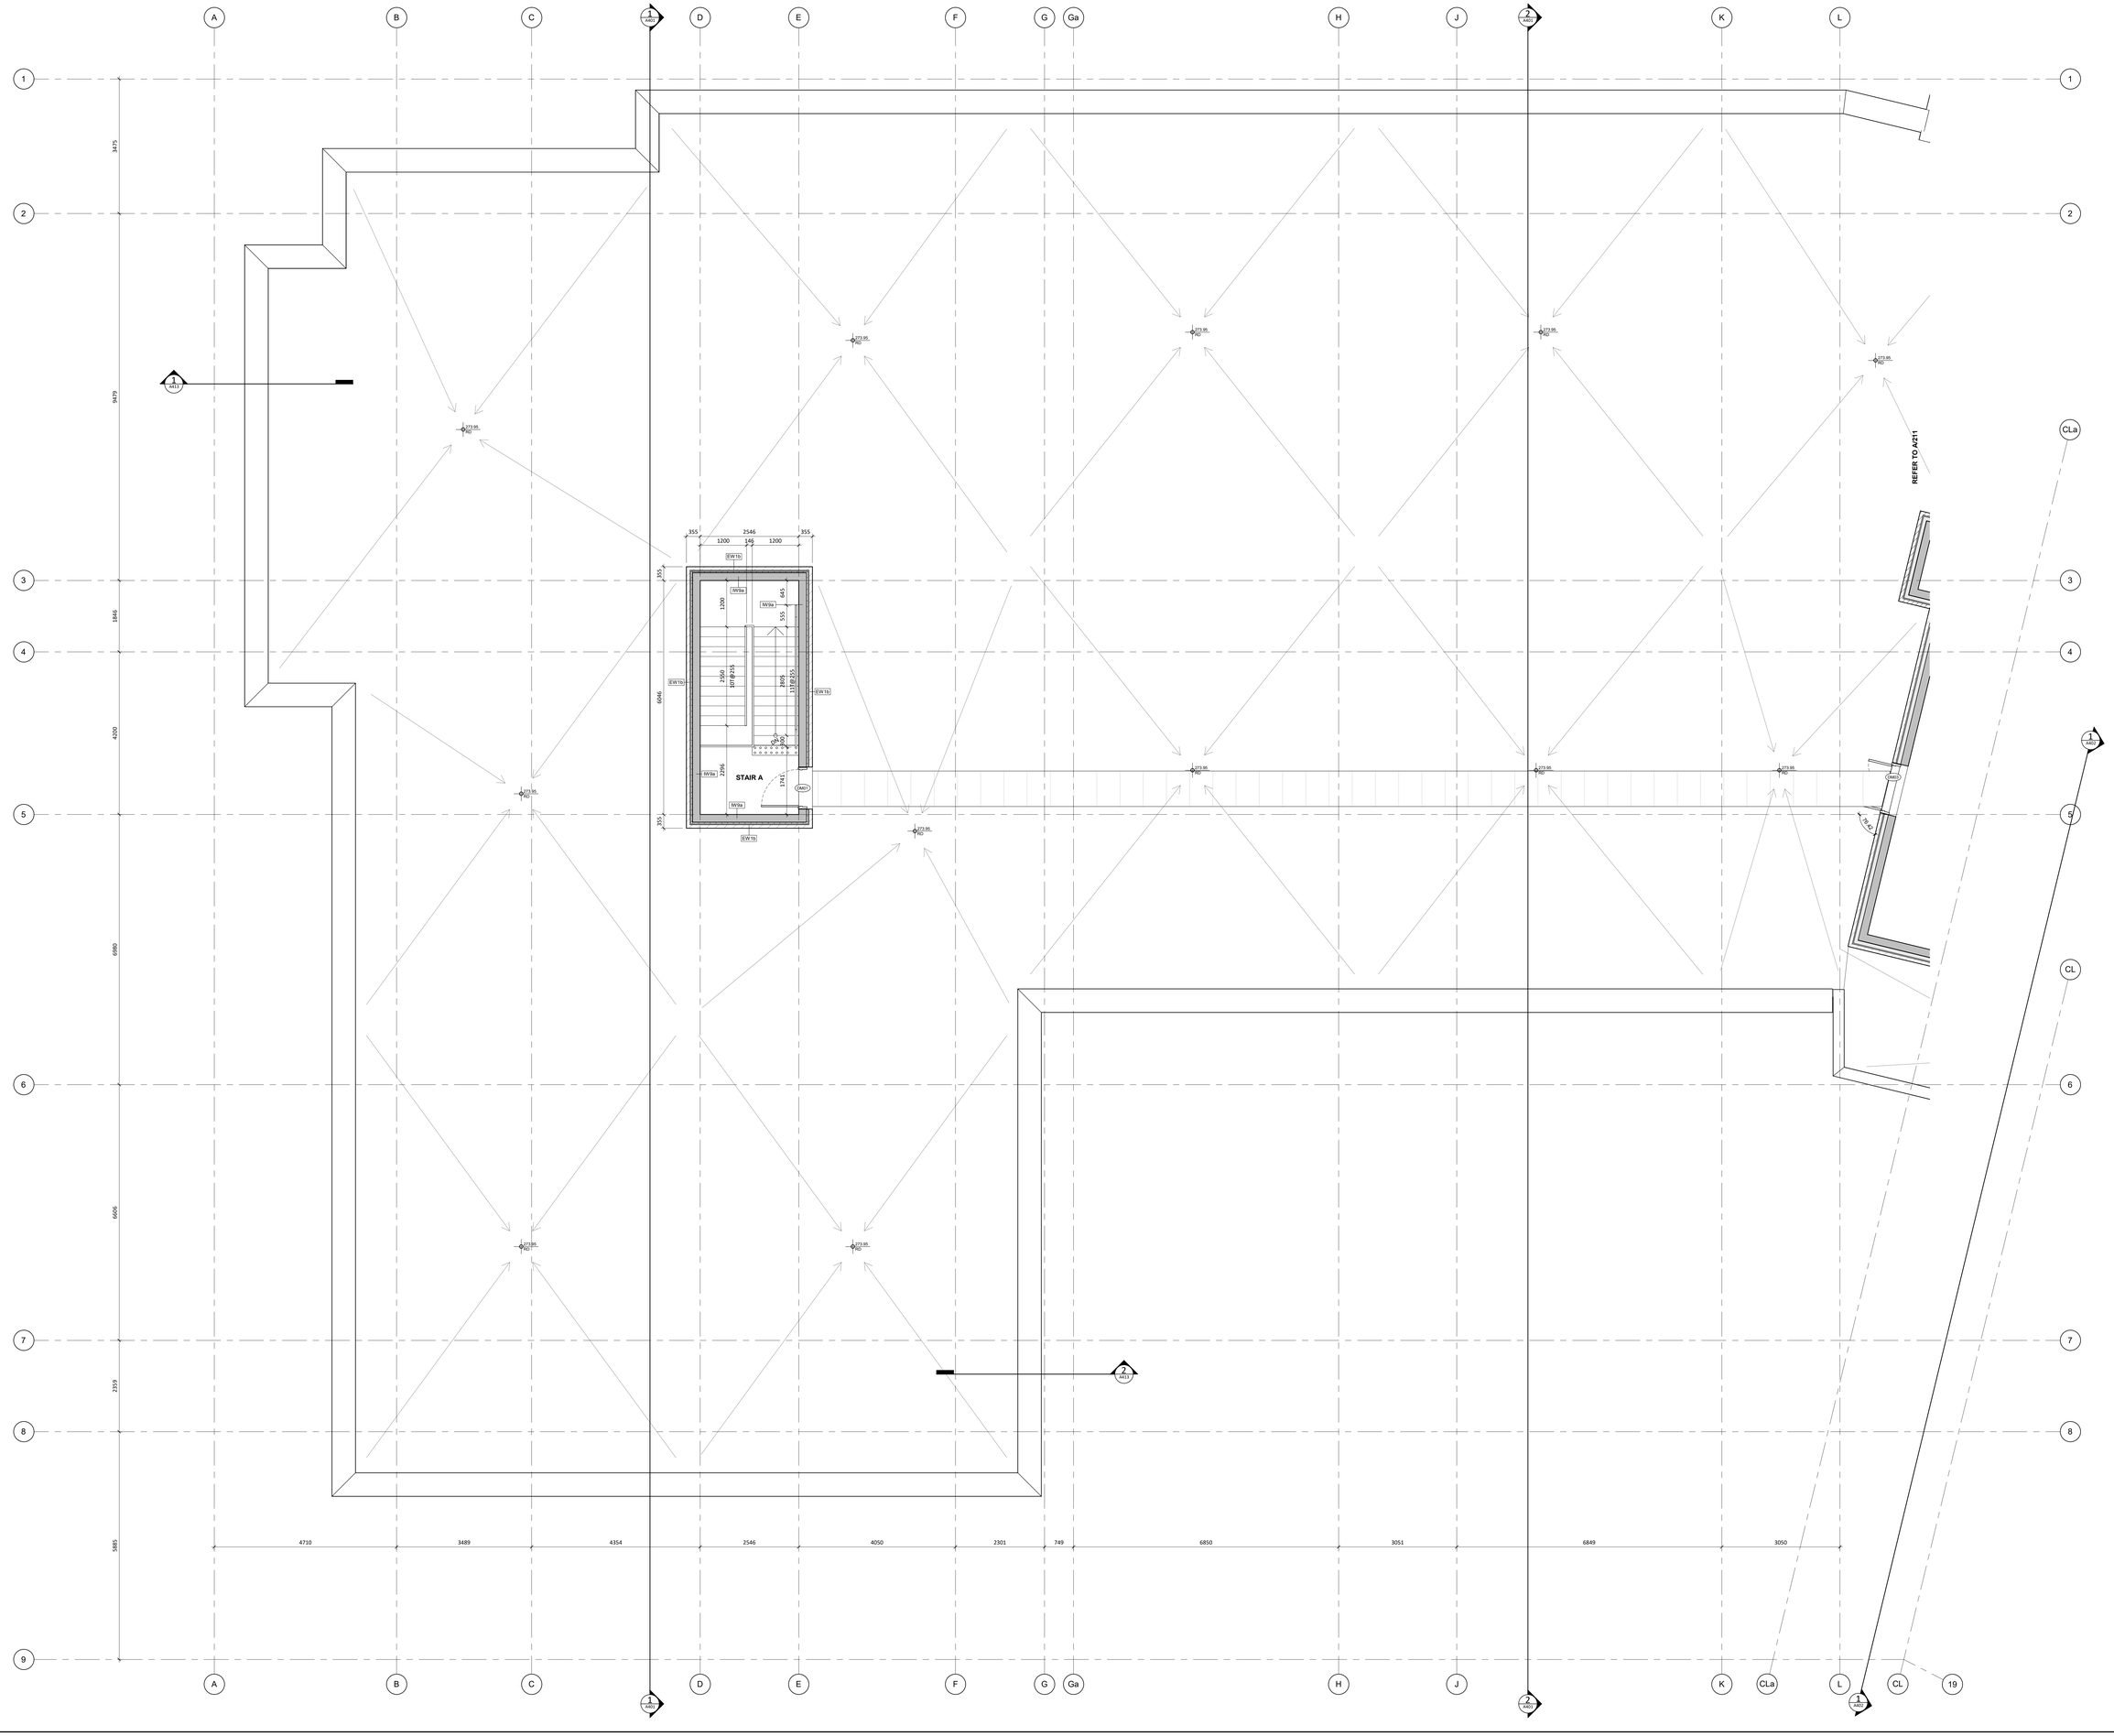

TURNER FLEISCHER

Turner Fleischer Architects Inc.

67 Lesmill Road
Toronto, ON, M3B 2T8
T 416 425 2222
turnerfleischer.com

This drawing, as an instrument of service, is provided by and is the property of Turner Fleischer Architects Inc. All rights including copyright are reserved by Turner Fleischer Architects Inc. Contractors shall verify and take dimensions on site and must notify Turner Fleischer Architects Inc. of any variations from the supplied information. This drawing is not to be scaled. The architect is not responsible for the accuracy of any information regarding existing conditions, including but not limited to, dimensions, which are to be verified by appropriate consultant's drawings before proceeding with the work. Construction must conform to all applicable codes and requirements of authorities having jurisdiction. The contractor working from drawings and specifications issued for construction shall assume full responsibility and bear costs for any corrections or damages resulting from his work.

#	DATE	DESCRIPTION	BY
1	2021-12-20	ISSUED FOR BUILDING PERMIT	CJF

TKG
TheKawarthaGroup

PROJECT

THE MOORINGS ON CAMERON LAKE

99 LOUISA STREET, FENELON FALLS, ON

DRAWING

MECHANICAL PENTHOUSE - A

PROJECT NO.
21.001CS

PROJECT DATE
2021-05-01

DRAWN BY
CJF

CHECKED BY
MY

SCALE
As indicated

DRAWING NO. A210

REV 1

2022-02-22 12:24:41 PM