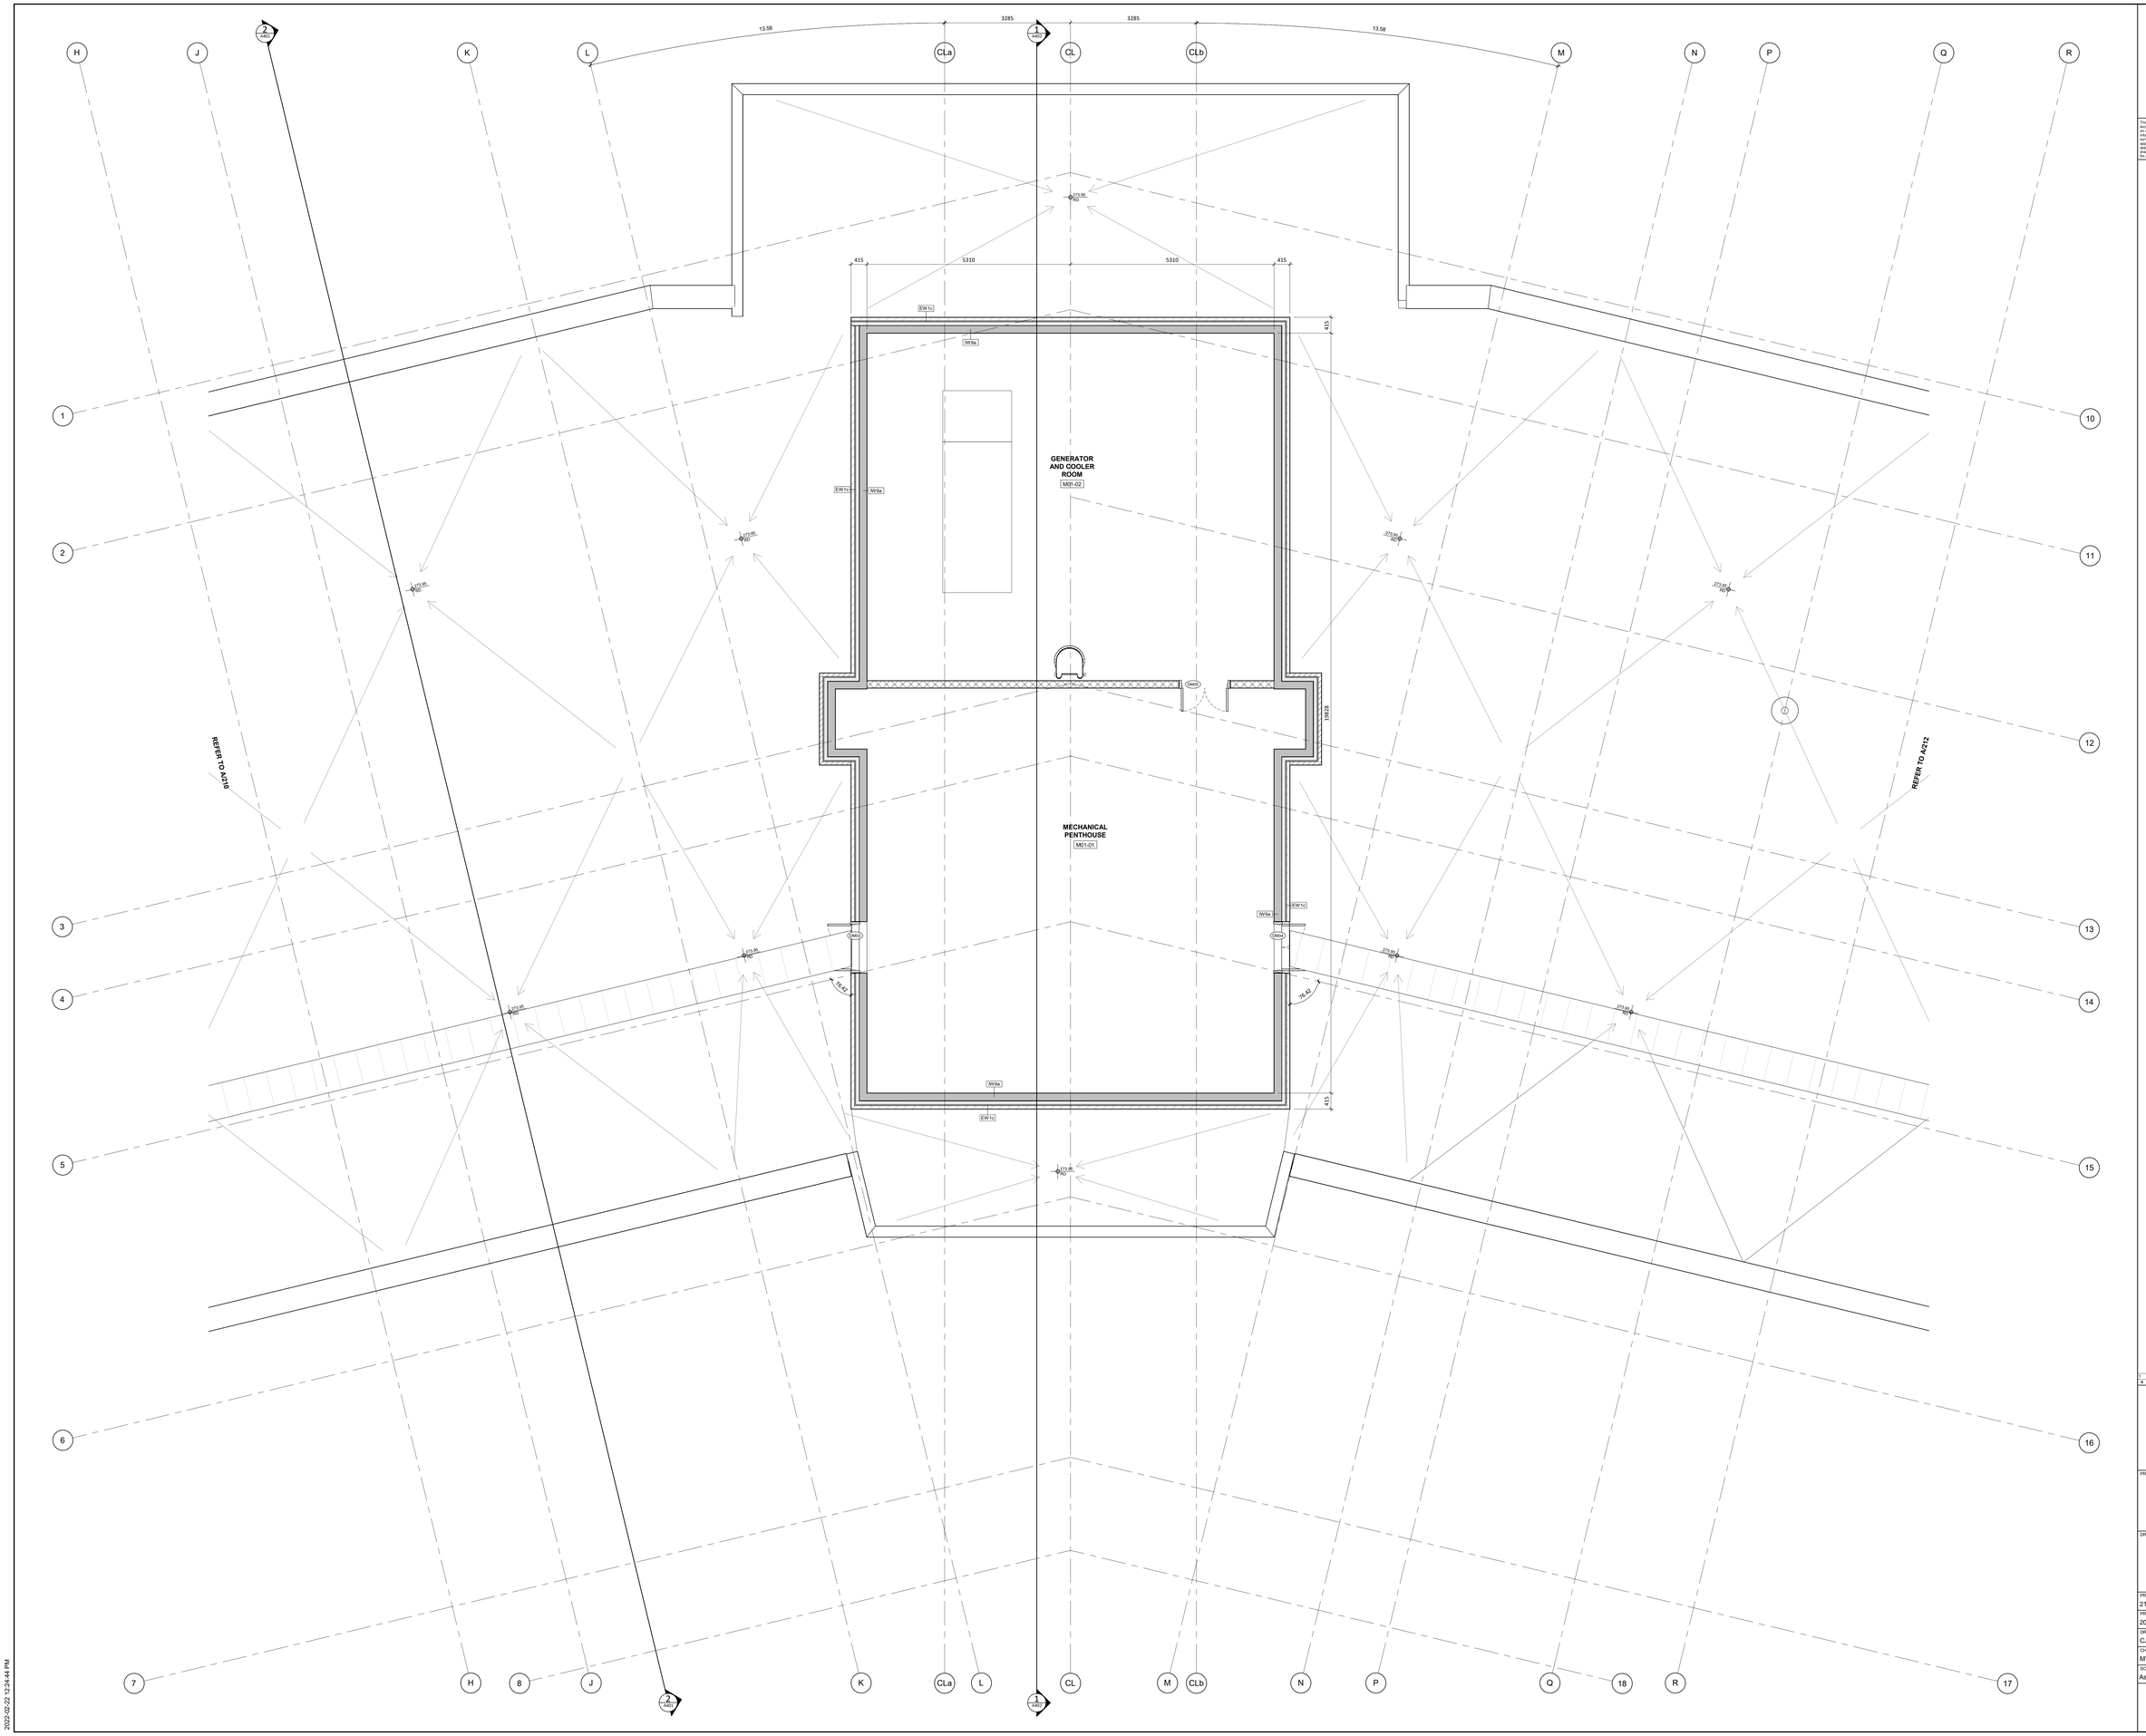

TURNER FLEISCHER

Turner Fleischer Architects Inc.

67 Lesmill Road
Toronto, ON, M3B 2T8
T 416 425 2222
turnerfleischer.com

This drawing, as an instrument of service, is provided by and is the property of Turner Fleischer Architects Inc. All rights including copyright are reserved by Turner Fleischer Architects Inc. Contractors shall verify and take ownership of all dimensions on site and must notify Turner Fleischer Architects Inc. of any variations from the supplied information. This drawing is not to be scaled. The architect is not responsible for the accuracy of any information shown on this drawing received from other consultants. Contractors must use the appropriate consultant's drawings before proceeding with the work. Construction must conform to all applicable codes and requirements of authorities having jurisdiction. The contractor working from drawings and specifications issued for construction must assume full responsibility and bear costs for any corrections or damages resulting from his work.

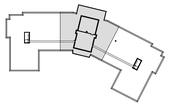

#	DATE	DESCRIPTION	BY
1	2021-12-20	ISSUED FOR BUILDING PERMIT	CJF

TKG TheKawarthaGroup

PROJECT

THE MOORINGS ON CAMERON LAKE

99 LOUISA STREET, FENELON FALLS, ON

DRAWING

MECHANICAL PENTHOUSE - B

PROJECT NO.	21.001CS
PROJECT DATE	2021-05-01
DRAWN BY	CJF
CHECKED BY	MY
SCALE	As indicated
DRAWING NO.	A211
REV.	1

2022-02-22 12:24:44 PM