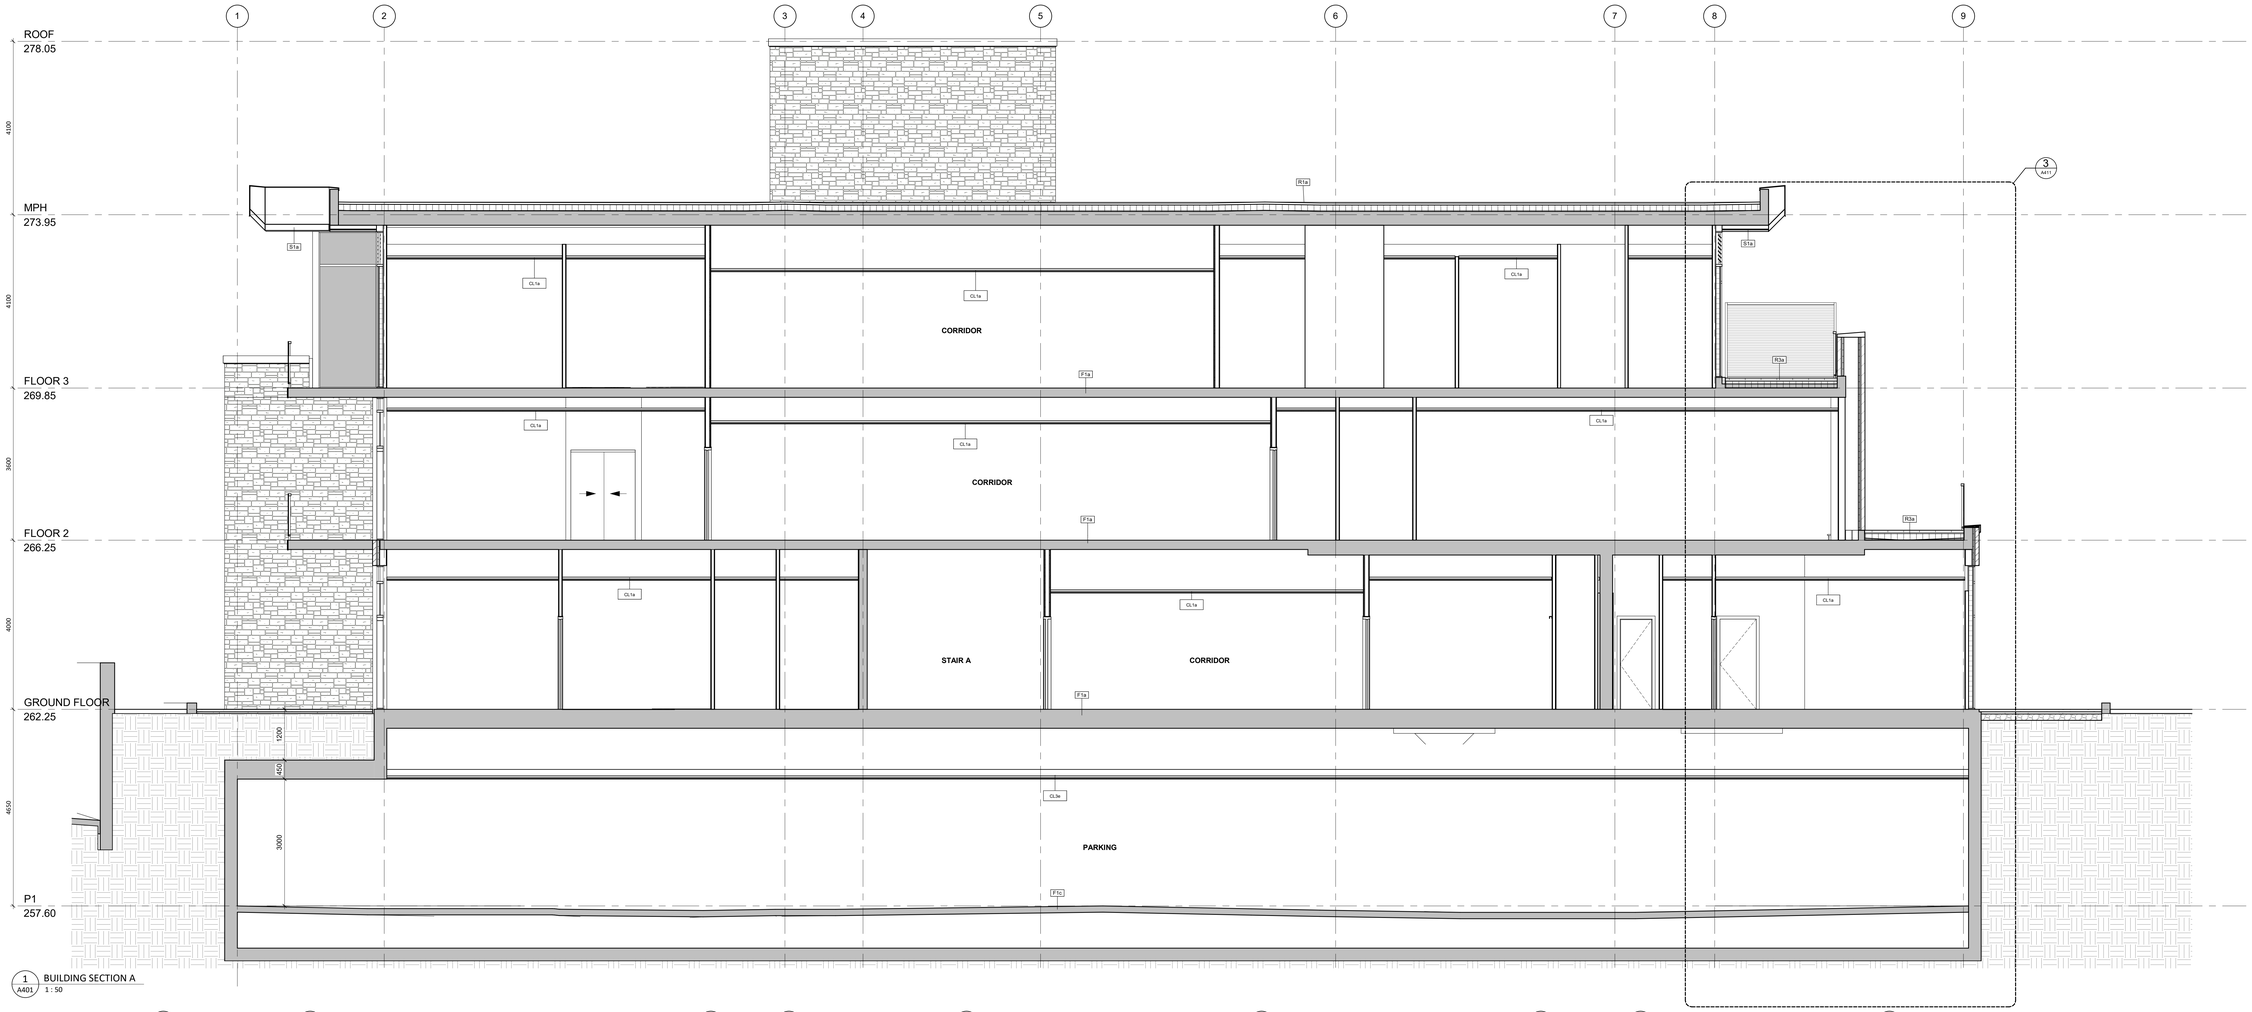

1 A401 BUILDING SECTION A
1 : 50

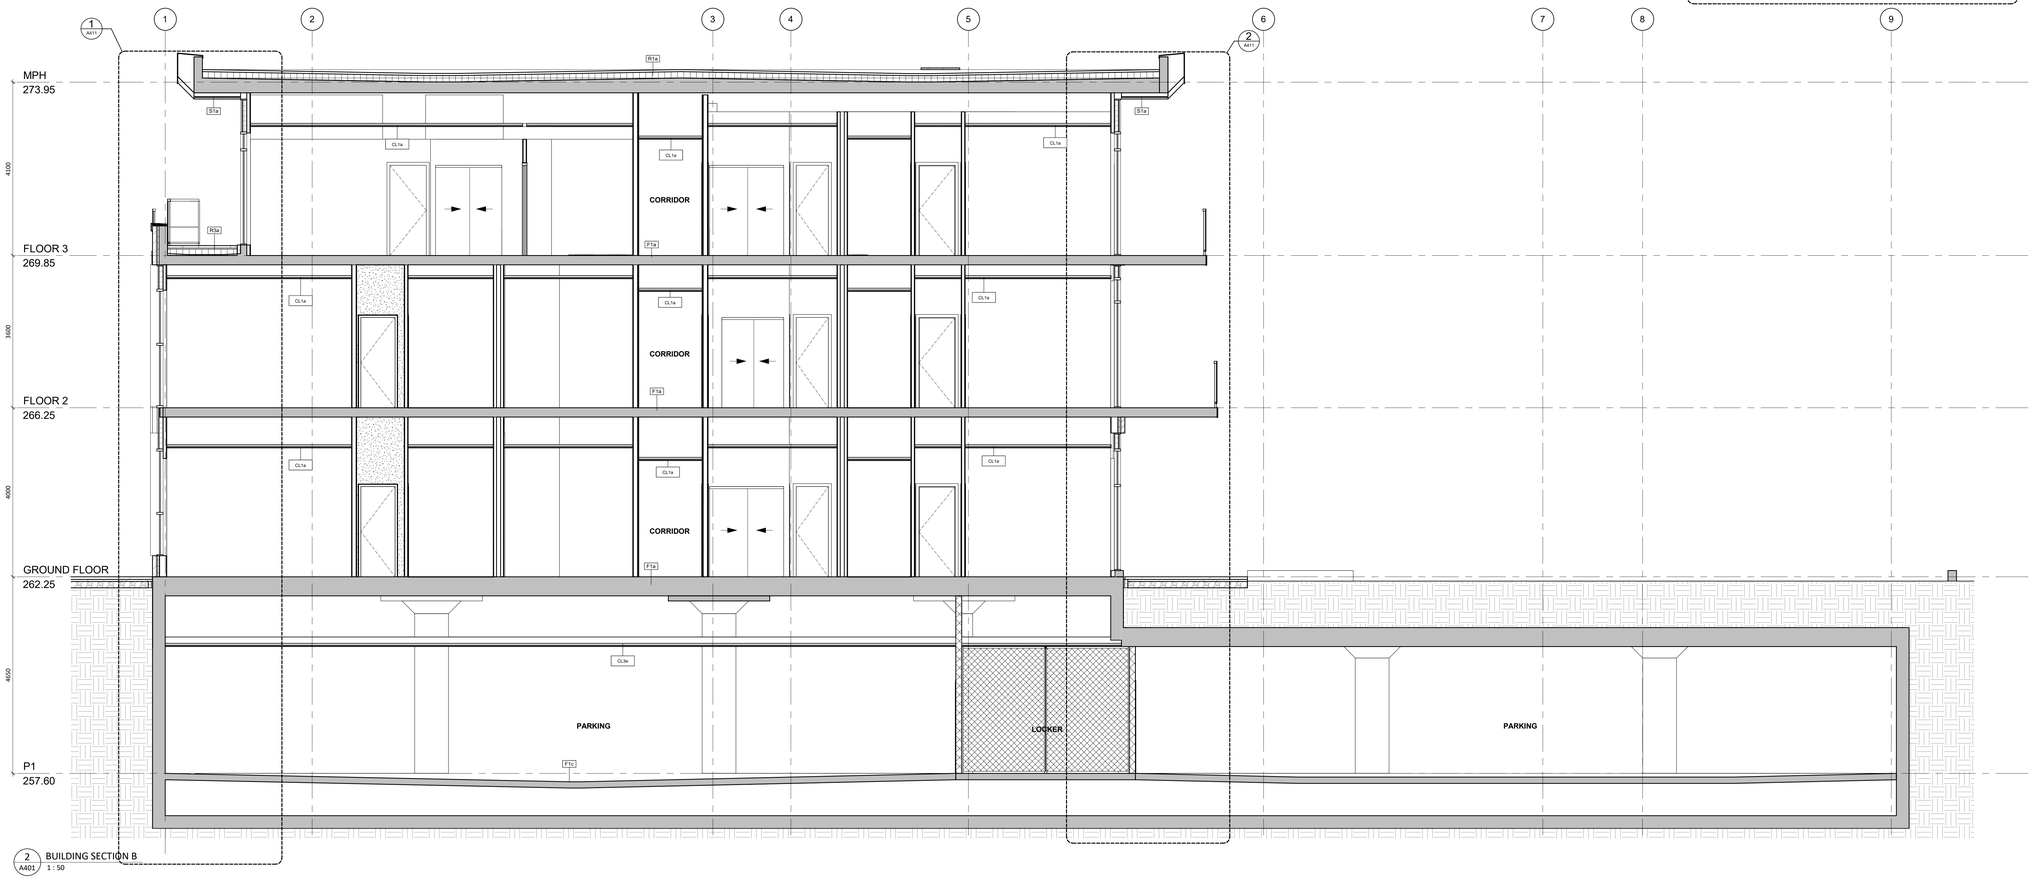

2 A401 BUILDING SECTION B
1 : 50

This drawing, as an instrument of service, is provided by and is the property of Turner Fleischer Architects Inc. and may not be used without the consent of Turner Fleischer Architects Inc. Contractor shall verify and accept responsibility for all dimensions on site and must notify Turner Fleischer Architects Inc. of any variations from the supplied information. This drawing is not to be scaled. The architect is not responsible for the accuracy of CAD files prepared for other consultants or contractors. Contractor shall verify all data in CAD files with the appropriate consultant's drawings before proceeding with the work. Construction must conform to all applicable codes and requirements of authorities having jurisdiction. The contractor working from consultants' drawings and specifications is deemed to accept and assume full responsibility and bear costs for any corrections or damages resulting from his work.

#	DATE	DESCRIPTION	BY
1	2021-12-20	ISSUED FOR BUILDING PERMIT	CJF

DRAWING

BUILDING SECTIONS

PROJECT NO.	21.001CS
PROJECT DATE	2021-05-01
DRAWN BY	CJF
CHECKED BY	MY
SCALE	1 : 50
DRAWING NO.	A401
REV.	1

2022-02-22 12:27:21 PM