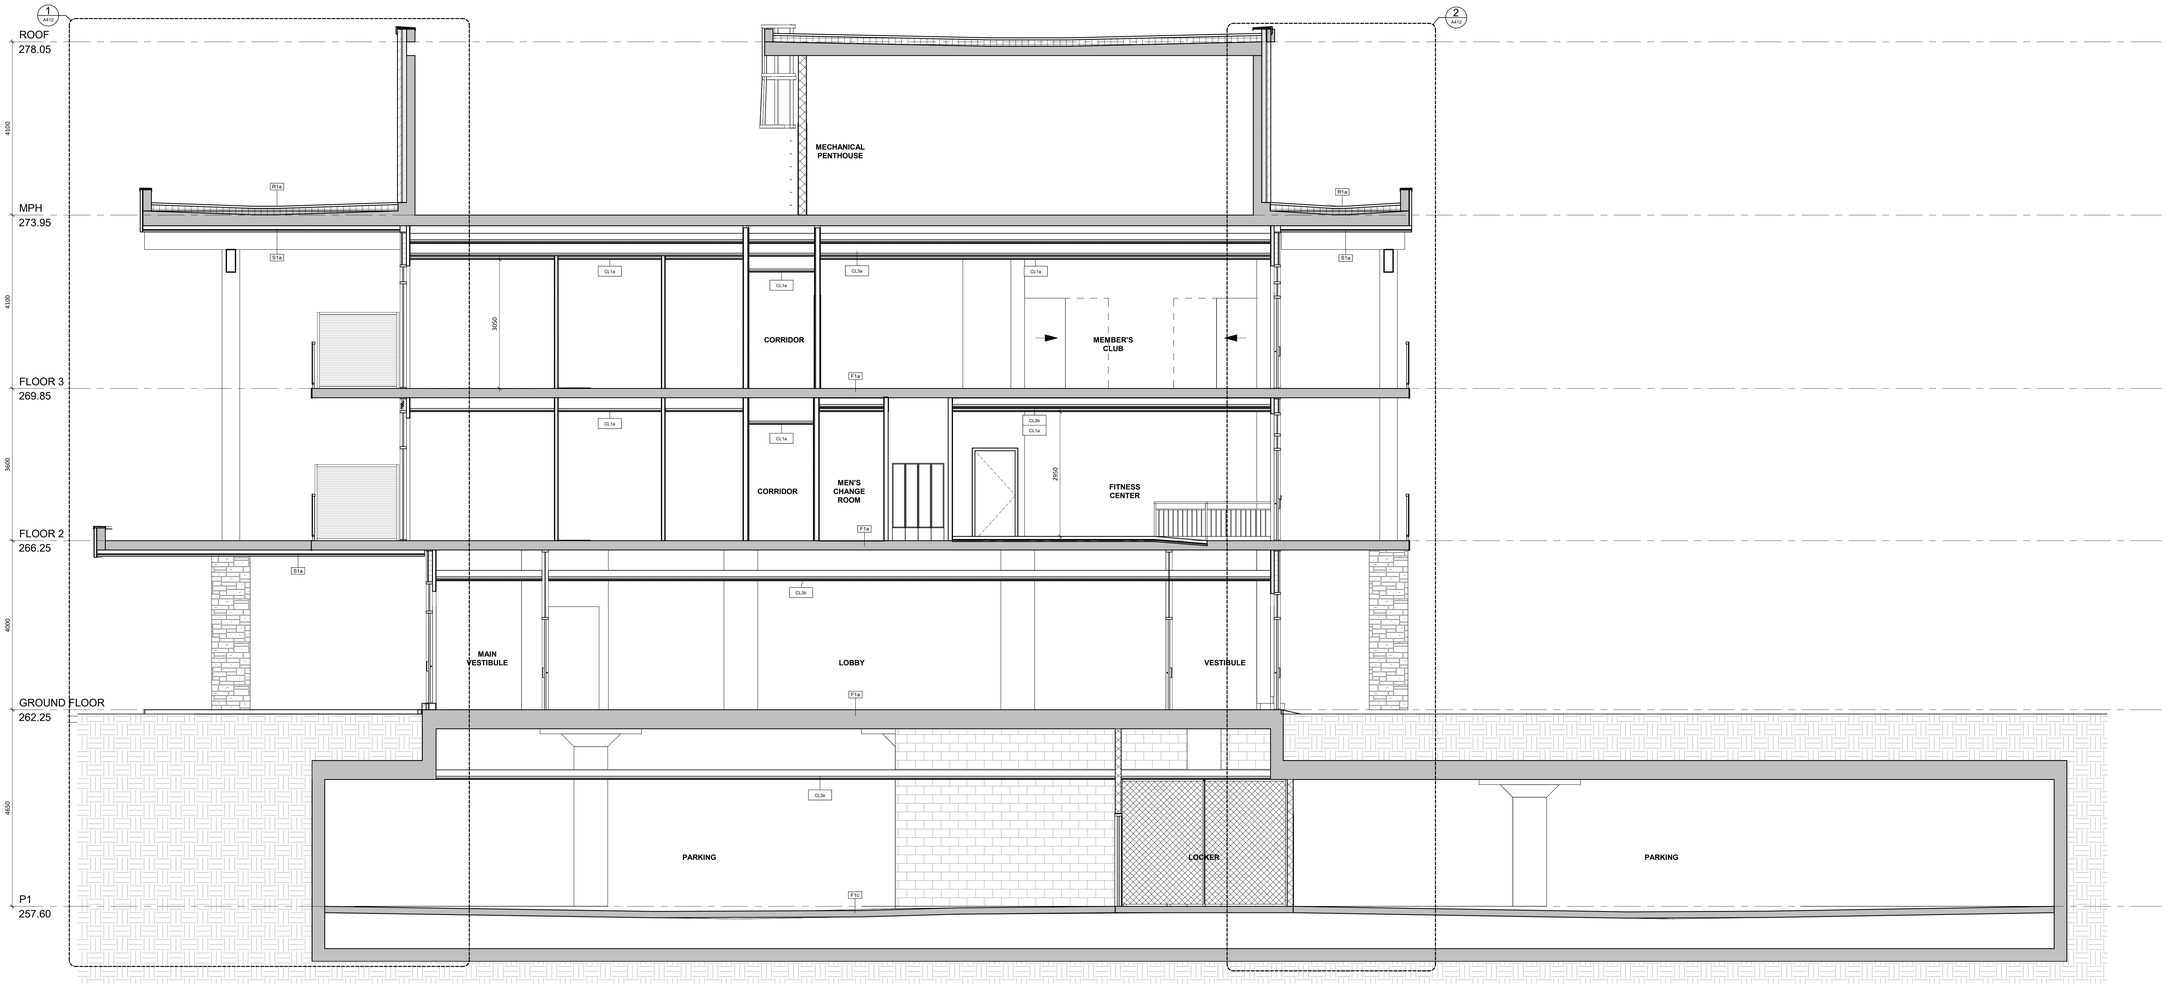

1 A402 BUILDING SECTION C
1 : 50

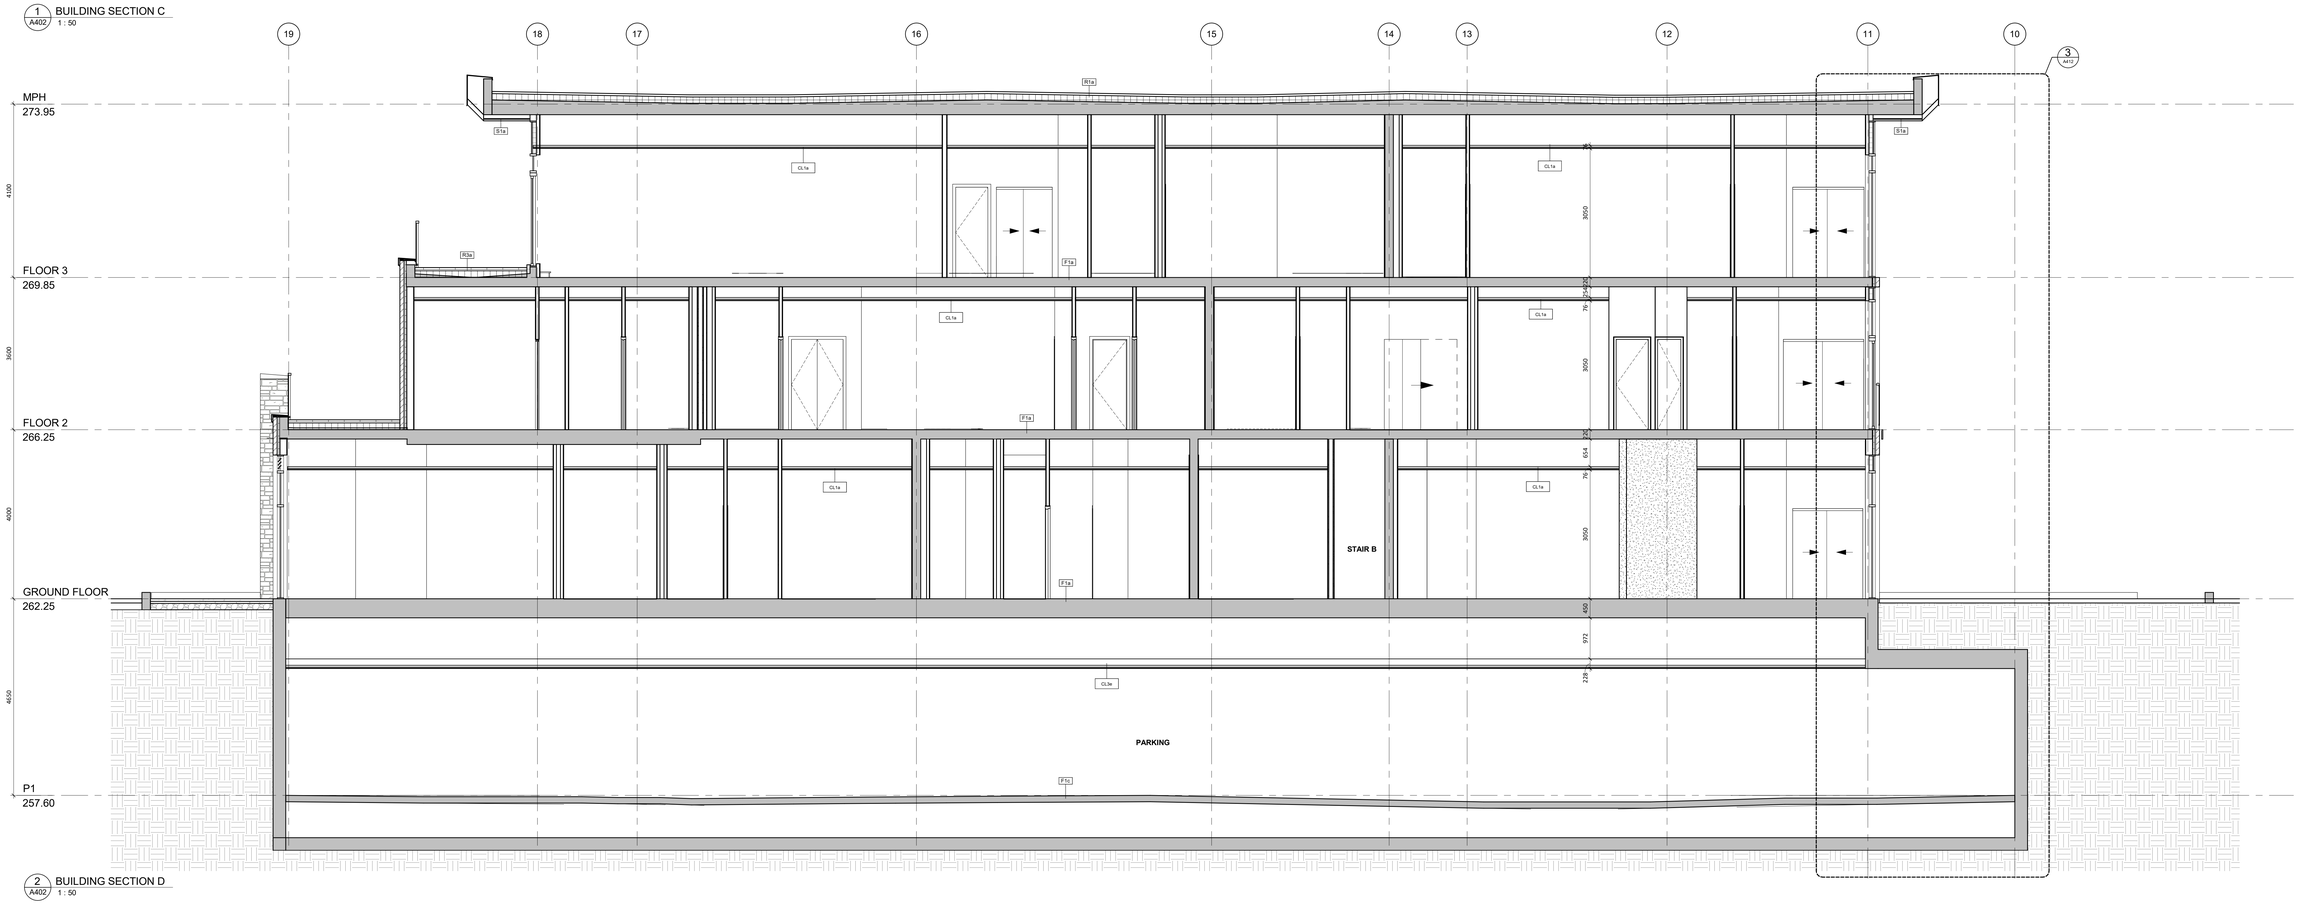

2 A402 BUILDING SECTION D
1 : 50

This drawing, as an instrument of service, is provided by and is the property of Turner Fleischer Architects Inc. and is to be returned on demand. Information shown on this drawing is to be verified on site and must notify Turner Fleischer Architects Inc. of any variations from the supplied information. This drawing is not to be scaled. The architect is not responsible for the accuracy of any information shown on subconsultant's drawings. Contractor shall review all drawings of all appropriate consultant's drawings before proceeding with the work. Construction must conform to all applicable codes and requirements of authorities having jurisdiction. The contractor working from these drawings is responsible for all dimensions. He must assume full responsibility and bear costs for any corrections or damages resulting from his work.

DRAWING
BUILDING SECTIONS

PROJECT NO.	21.001CS
PROJECT DATE	2021-05-01
DRAWN BY	CJF
CHECKED BY	MY
SCALE	1 : 50
DRAWING NO.	A402
REV.	1

2022-02-22 12:27:24 PM