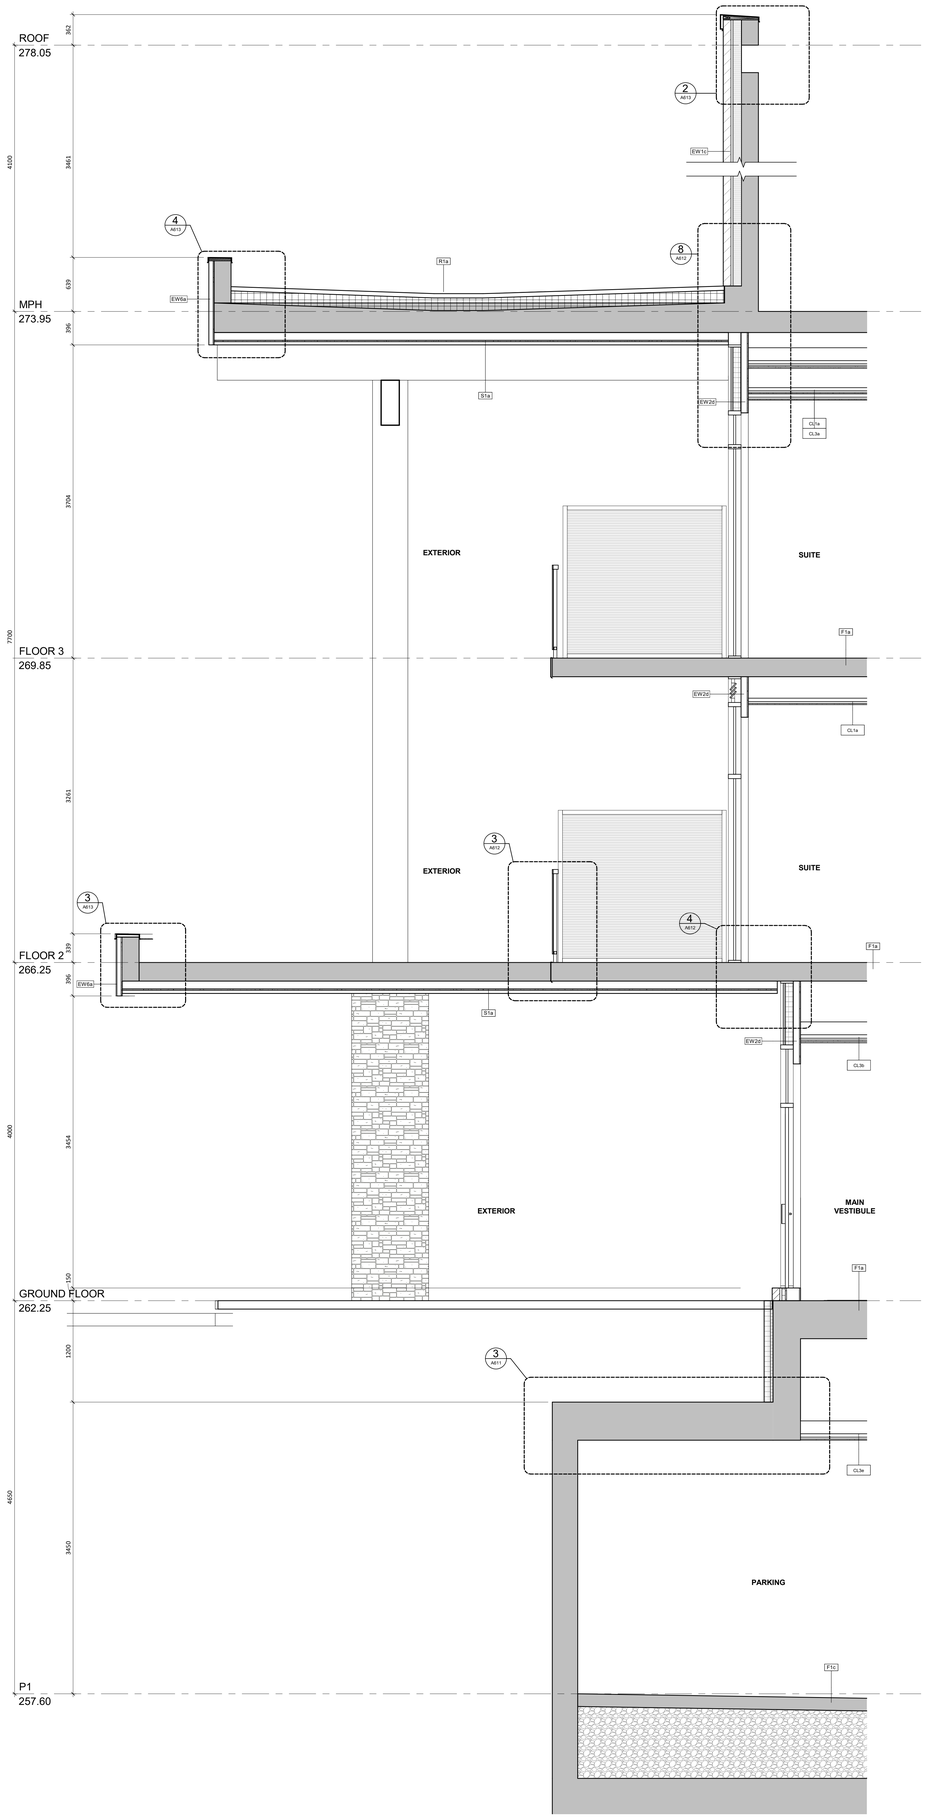

1 A412 WALL SECTION 4
1 : 25

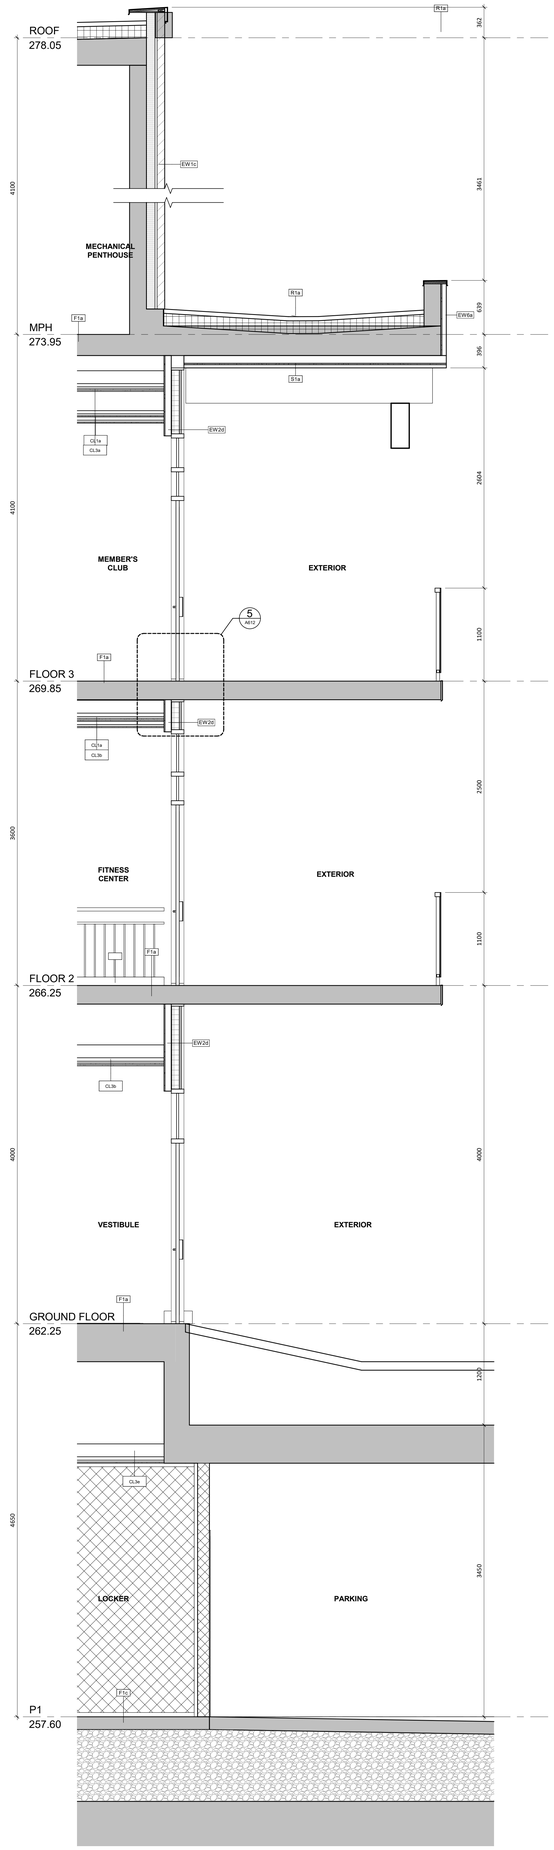

2 A412 WALL SECTION 5
1 : 25

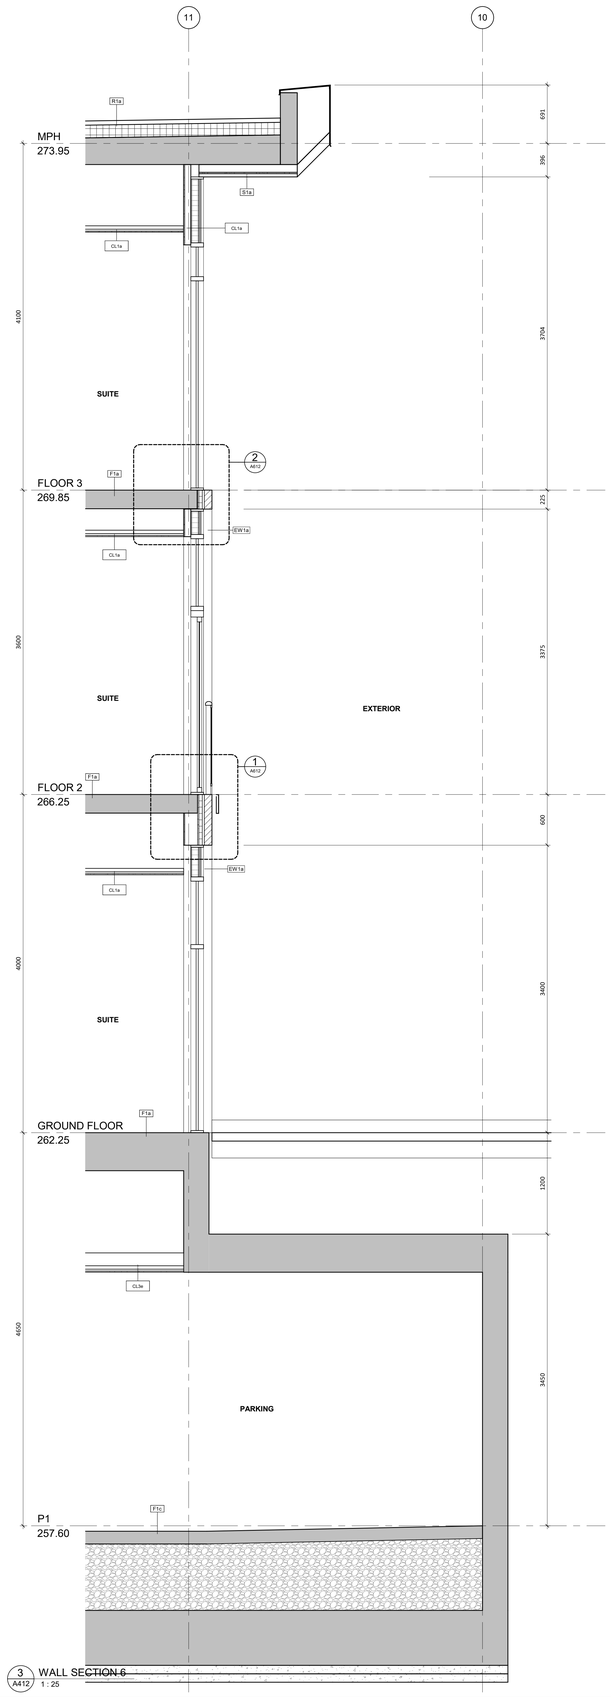

3 A412 WALL SECTION 6
1 : 25

This drawing, as an instrument of service, is provided by and is the property of Turner Fleischer Architects Inc. and may not be used or reproduced without consent of Turner Fleischer Architects Inc. Contractors on site and must notify Turner Fleischer Architects Inc. of any variations from the supplied information. This drawing is not to be scaled. The architect is not responsible for the accuracy of data from other consultants or suppliers. Contractor must verify and accept all data on the appropriate consultant's drawings before proceeding with the work. Construction must conform to all applicable codes and requirements of authorities having jurisdiction. The contractor working from drawings and specifications issued for construction must assume full responsibility and bear costs for any corrections or damages resulting from his work.

PROJECT

DRAWING
WALL SECTIONS

PROJECT NO.	21.001CS
PROJECT DATE	2021-05-01
DRAWN BY	CJF
CHECKED BY	MY
SCALE	1 : 25
DRAWING NO.	A412
REV.	

2022-02-22 12:27:33 PM