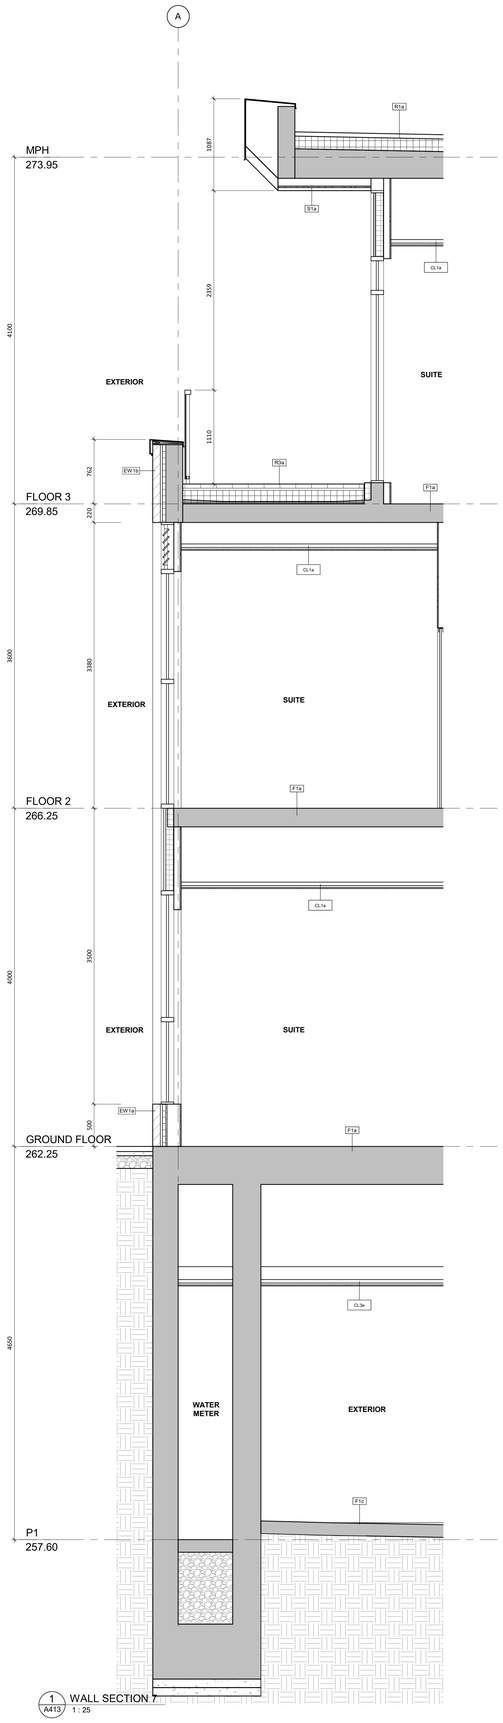

1 A413 WALL SECTION 7
1 : 25

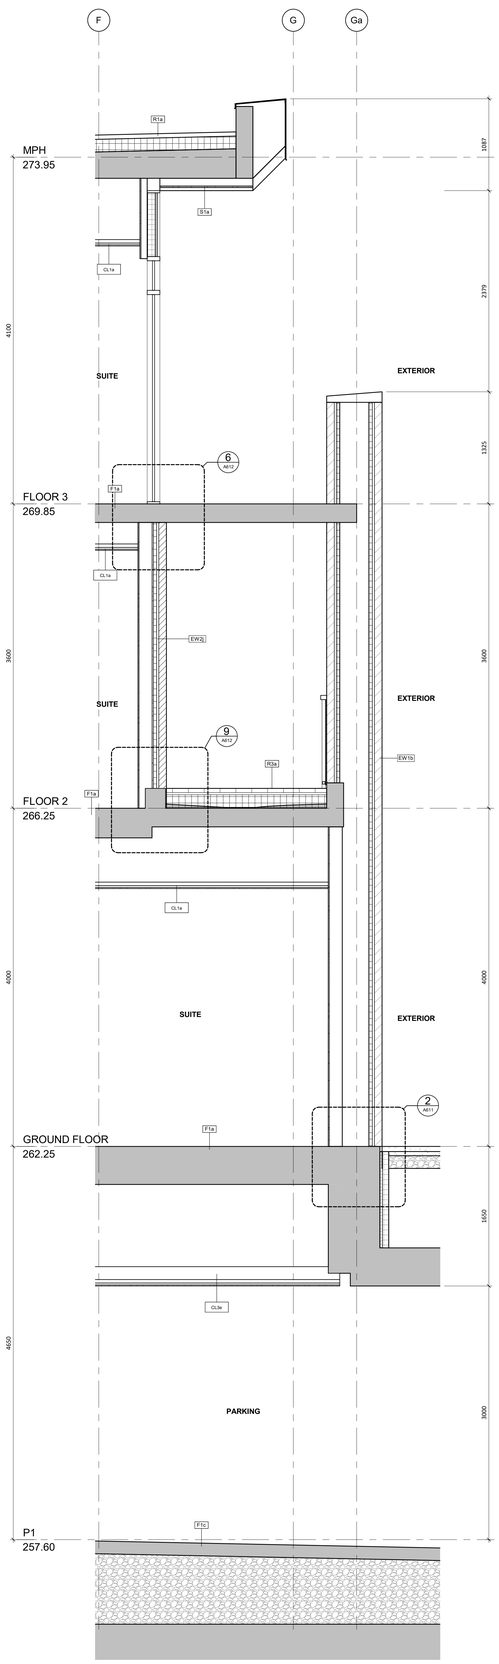

2 A413 WALL SECTION 8
1 : 25

This drawing, as an instrument of service, is provided by and is the property of Turner Fleischer Architects Inc. and is to be returned on request and at completion of the work. Contractor shall verify all conditions on site and must notify Turner Fleischer Architects Inc. of any variations from the supplied information. This drawing is not to be scaled. The architect is not responsible for the accuracy of CAD files prepared for other parties. Contractor shall be responsible for checking all CAD files against the appropriate consultant's drawings before proceeding with the work. Construction must conform to all applicable codes and requirements of authorities having jurisdiction. The contractor working from these drawings shall confirm that he has the skill and knowledge and assume full responsibility and bear costs for any corrections or damages resulting from his work.

DRAWING
WALL SECTIONS

PROJECT NO	21.001CS
PROJECT DATE	2021-05-01
DRAWN BY	CJF
CHECKED BY	MY
SCALE	1 : 25
DRAWING NO	A413
REV.	

2022-02-22 10:27:36 PM