DOOR SCHEDULE

DOOR NUMBER	From	WALL FIRE RATING	To	FIRE RATING	TEMP. RISE	SIZE WIDTH	SIZE HEIGHT	SIZE THICKNESS	DOOR TYPE	DOOR MATERIAL	DOOR FINISH	DOOR GLAZING	FRAME MATERIAL	FRAME FINISH	FRAME THRESHOLD	HARDWARE POWER OPERATOR	HARDWARE EXIT DEVICE	HARDWARE KICKPLATE	HARDWARE LOCK	HARDWARE PUSH/PULL	HARDWARE LATCH	HARDWARE WEATHERSTRIPPING	SECURITY CARD SWIPE	SECURITY ELECTRIC STRIKE	SECURITY MAGLOCK	COMMENTS
P1																										
D118	PARKING		LOCKER	1 HR		965	2135	45	A1																	
DB00	PARKING	-	EXTERIOR	-		5800	2135	40	G1	INSULATED METAL	PAINT	-	METAL	PAINT	-	•						•				
DB01	PARKING	1 HR	INTAKE SHAFT	45 MIN		965	2135	35	A1	HC METAL	PAINT	-	METAL	PAINT	-			•			•					
DB02	PARKING	0 HR	VESTIBULE	0 HR		965	2135	35	A2	HC METAL	PAINT	-	METAL	PAINT	-	•	•	•	•	•	•		•			
DB03	VESTIBULE	2 HR	STAIR C	1.5 HR		965	2135	35	A2	HC METAL	PAINT	-	METAL	PAINT	-		•	•		•	•					
DB04	VESTIBULE	2 HR	ELEV. LOBBY	1.5 HR		965	2135	35	A2	HC METAL	PAINT	-	METAL	PAINT	-	•	•	•	•	•	•		•			
DB05	ELEV. LOBBY	1.5 HR	LOCKERS (4)	1 HR		965	2135	45	A1	HC METAL	PAINT	-	METAL	PAINT	-			•	•		•		•			
DB06	ELEV. MACHINE ROOM		ELEV. LOBBY	1.5 HR		965	2135	35	A1																	
DB07	PARKING		LOCKER	1 HR		965	2135	45	A1																	
DB08	PARKING	1 HR	EXHAUST SHAFT	45 MIN		965	2135	35	A1	HC METAL	PAINT	-	METAL	PAINT	-				•		•					
DB09	PARKING	0 HR	VESTIBULE	0 HR		965	2135	35	A2	HC METAL	PAINT	-	METAL	PAINT	-		•	•		•	•					
DB10	VESTIBULE	2 HR	STAIR B	1.5 HR		965	2135	35	A2	HC METAL	PAINT	-	METAL	PAINT	-		•	•		•	•					
DB11	LOCKERS (5)	1.5 HR	PARKING	1 HR		965	2135	45	A1	HC METAL	PAINT	-	METAL	PAINT	-			•	•		•		•			
DB12	ELECTRICAL ROOM	2 HR	PARKING	1.5 HR		965	2135	35	A1	HC METAL	PAINT	-	METAL	PAINT	-				•		•					
DB13	PARKING	2 HR	TELECOM ROOM	1.5 HR		965	2135	35	A1	HC METAL	PAINT	-	METAL	PAINT	-				•		•					
DB14	PARKING	2 HR	WATER METER	1.5 HR		965	2135	35	A1	HC METAL	PAINT	-	METAL	PAINT	-				•		•					
DB15	PARKING	0 HR	VESTIBULE	0 HR		965	2135	35	A2	HC METAL	PAINT	-	METAL	PAINT	-		•	•		•	•					
DB16	STAIR A	2 HR	VESTIBULE	1.5 HR		965	2135	35	A2	HC METAL	PAINT	-	METAL	PAINT	-		•	•		•	•					
GROUND FLOOR																										
D100	MAIN VESTIBULE	-	EXTERIOR	-		1830	2135	45	B6	ALUM.	ANODIZED	•	ALUM.	ANODIZED	METAL	•				•	•	•	•			EXTERIOR ALUMINUM DOOR/FRAME w/ GLAZING
D101	LOBBY	-	MAIN VESTIBULE	-		1830	2135	35	B6	ALUM.	ANODIZED	•	ALUM.	ANODIZED	METAL	•			•	•	•		•			EXTERIOR ALUMINUM DOOR/FRAME w/ GLAZING
D102	MAIL LOADING	-	EXTERIOR	-		915	2135	45	A6	ALUM.	ANODIZED	•	ALUM.	ANODIZED	METAL				•		•	•				
D103	LOBBY	1.5 HR	PARCEL STORAGE	1 HR		965	2135	35	A1	HC METAL	PAINT	-	METAL	PAINT	-				•		•		•			
D104	LOBBY	1.5 HR	MOVING ROOM	1 HR		965	2135	35	A1	HC METAL	PAINT	-	METAL	PAINT	-				•		•		•			
D105	EXTERIOR	-	MOVING ROOM	-		1850	2135	35	B6	ALUM.	ANODIZED	•	ALUM.	ANODIZED	METAL				•		•	•				
D106	MOVING ROOM	2 HR	VESTIBULE	1.5 HR		965	2135	35	A1	HC METAL	PAINT	-	METAL	PAINT	-			•	•		•					
D107	GARBAGE ROOM	-	VESTIBULE	-		965	2135	35	A1	HC METAL	PAINT	-	METAL	PAINT	-			•			•					
D108	EXTERIOR	-	STAIR C	-		860	2135	45	A6	ALUM.	ANODIZED	•	ALUM.	ANODIZED	METAL		•		•		•	•				
D109	GARBAGE ROOM	-	EXTERIOR	-		1830	2440	38	G1	INSULATED METAL	PAINT	-	METAL	PAINT					•		•	•				
D110	EXTERIOR	-	STAIR B	-		965	2135	45	A6	ALUM.	ANODIZED	•	ALUM.	ANODIZED	METAL		•		•		•	•				
D111	VESTIBULE	-	LOBBY	-		1830	2135	35	B6	ALUM.	ANODIZED	•	ALUM.	ANODIZED	METAL	•			•	•	•		•			EXTERIOR ALUMINUM DOOR/FRAME w/ GLAZING
D112	EXTERIOR	-	VESTIBULE	-		1830	2135	45	B6	ALUM.	ANODIZED	•	ALUM.	ANODIZED	METAL	•			•	•	•	•				EXTERIOR ALUMINUM DOOR/FRAME w/ GLAZING
D113	STAIR A	-	EXTERIOR	-		965	2110	45	A6	ALUM.	ANODIZED	•	ALUM.	ANODIZED	METAL		•		•		•	•				
D114	LOBBY	-	UNIVERSAL WASHROOM	-		965	2135	35	A1	HC METAL	PAINT	-	METAL	PAINT	-			•	•	•	•					
D115	PET SPA	-	MAIN VESTIBULE	-		965	2135	35	A1	HC METAL	PAINT	-	METAL	PAINT	-				•		•		•			
D116	HEAT PUMP CLOSET	-	PET SPA	-		760	2135	35	A1	HC METAL	PAINT	-	METAL	PAINT	-					•	•					
D117	PET SPA	-	EXTERIOR	-		915	2135	45	A6	ALUM.	ANODIZED	•	ALUM.	ANODIZED	METAL	•			•	•	•		•			
FLOOR 2																										
D200	CORRIDOR	1 HR	FITNESS CENTER	45 MIN		965	2135	35	A1	HOLLOW METAL	PAINT	-	METAL	PAINT	-	•			•		•		•			
D201	FITNESS CENTER	-	CLOSET	-		965	2135	35	A1	HC WOOD	PAINT	-	WOOD	PAINT	-				•		•					
D202	FITNESS CENTER	-	MEN'S WASHROOM	-		965	2135	35	A1	HC WOOD	PAINT	-	WOOD	PAINT	-					•						
D203	MEN'S CHANGE ROOM	-	MEN'S WASHROOM	-		965	2135	35	A1	HC WOOD	PAINT	-	WOOD	PAINT	-					•						
D204	FITNESS CENTER	-	WOMEN'S WASHROOM	-		965	2135	35	A1	HC WOOD	PAINT	-	WOOD	PAINT	-					•						
D205	WOMEN'S WASHROOM	-	WOMEN'S CHANGE ROOM	-		965	2135	35	A1	HC WOOD	PAINT	-	WOOD	PAINT	-					•						
D206	EXTERIOR	-	FITNESS CENTER	-		1830	2135	45	B6	ALUM.	ANODIZED	•	ALUM.	ANODIZED	METAL	•			•		•	•				EXTERIOR ALUMINUM DOOR/FRAME w/ GLAZING
D207	FITNESS CENTER	-	YOGA	-		958	2135	35	A6	ALUM.	ANODIZED	•	ALUM.	ANODIZED	-					•						
D208	CLOSET	-	YOGA	-		965	2135	35	A1	HC WOOD	PAINT	-	WOOD	ANODIZED	-				•		•					
D209	SAUNA	-	YOGA	-		965	2135	35	-	-	-	-	-	-	-											SAUNA DOOR AS PER MANUFACTURERS SPECIFICATIONS
D210	HEAT PUMP CLOSET	-	FITNESS CENTER	-		760	2135	35	A1	HC WOOD	PAINT	-	WOOD	PAINT	-				•		•					
FLOOR 3																										
D300	CORRIDOR	1 HR	MEMBER'S CLUB	45 MIN		1220	2135	45	B1	HOLLOW METAL	PAINT	-	METAL	PAINT	-	•			•		•		•			
D301	CORRIDOR	1 HR	BARRIER FREE WASHROOM	45 MIN		965	2135	35	A1	HOLLOW METAL	PAINT	-	METAL	PAINT	-	•		•	•		•					
D302	CORRIDOR	1 HR	WASHROOM	45 MIN		965	2135	35	A1	HOLLOW METAL	PAINT	-	METAL	PAINT	-			•	•		•					
D303	HEAT PUMP CLOSET	-	MEMBER'S CLUB	-		760	2135	35	A1	HC WOOD	PAINT	-	WOOD	PAINT	-				•		•					
D304	MEMBER'S CLUB	-	MEMBER'S CLUB	-		965	2135	35	E1	HC WOOD	PAINT	-	WOOD	PAINT	-											POCKET DOOR (HOLLOW-CORE WOOD c/w MASONITE FINISH); TRACK & HANGERS: CROWDER FRAME "TYPE-C"; w/ EDGE LOCK & FLUSH PULLS
D305	MEMBER'S CLUB	-	MEMBER'S CLUB	-		965	2135	35	E1	HC WOOD	PAINT	-	WOOD	PAINT	-											POCKET DOOR (HOLLOW-CORE WOOD c/w MASONITE FINISH); TRACK & HANGERS: CROWDER FRAME "TYPE-C"; w/ EDGE LOCK & FLUSH PULLS
D306	EXTERIOR	-	MEMBER'S CLUB	-		1830	2135	45	B6	ALUM.	ANODIZED	•	ALUM.	ANODIZED	METAL	•			•	•	•	•				EXTERIOR ALUMINUM DOOR/FRAME w/ GLAZING
D307	MEMBER'S CLUB	-	TV ROOM	-		965	2135	35	A1	HC WOOD	PAINT	-	WOOD	PAINT	-					•	•					
MPH																										
DM01	ROOF	-	STAIR A	-		965	2135	35	A1	INSULATED METAL	PAINT	-	METAL	PAINT	METAL			•	•	•	•	•	•			
DM02	ROOF	-	STAIR B	-		965	2135	35	A1	INSULATED METAL	PAINT	-	METAL	PAINT	METAL			•	•	•	•	•	•			
DM03	MECHANICAL PENTHOUSE	-	ROOF	-		1220	2135	45	B1	INSULATED METAL	PAINT	-	METAL	PAINT	METAL			•		•	•	•	•			
DM04	ROOF	-	MECHANICAL PENTHOUSE	-		1220	2135	45	B1	INSULATED METAL	PAINT	-	METAL	PAINT	METAL			•		•	•	•				
DM05	GENERATOR AND COOLER ROOM	-	MECHANICAL PENTHOUSE	-		1220	2135	45	B1	INSULATED METAL	PAINT	-	METAL	PAINT	METAL			•		•	•	•				

DOOR SCHEDULE - SUITES

DOOR NUMBER	LOCATION	FIRE RATING	SIZE WIDTH	SIZE HEIGHT	SIZE THICKNESS	DOOR TYPE	DOOR MATERIAL	DOOR FINISH	DOOR GLAZING	FRAME MATERIAL	FRAME FINISH	FRAME THRESHOLD	HARDWARE LOCK	HARDWARE LATCH	HARDWARE PRIVACY SET	HARDWARE PUSH/PULL	COMMENTS
S01a	SUITE ENTRY	20 MIN	965	2135	35	A1	SC WOOD	PAINT	-	STEEL	PAINT	WOOD	•	•			Door viewer, single rabbet slip-on frame, undercut
S02a	BEDROOM	-	915	2135	35	A1	HC WOOD	PAINT	-	WOOD	PAINT	-		•			
S02b	BEDROOM	-	860	2135	35	A1	HC WOOD	PAINT	-	WOOD	PAINT	-		•			
S02c	BEDROOM	-	810	2135	35	A1	HC WOOD	PAINT	-	WOOD	PAINT	-		•			
S03a	BATHROOM	-	915	2135	35	A1	HC WOOD	PAINT	-	WOOD	PAINT	-		•	•		
S03b	BATHROOM	-	860	2135	35	A1	HC WOOD	PAINT	-	WOOD	PAINT	-		•	•		
S03c	BATHROOM	-	810	2135	35	A1	HC WOOD	PAINT	-	WOOD	PAINT	-		•	•		
S03d	BATHROOM	-	760	2135	35	A1	HC WOOD	PAINT	-	WOOD	PAINT	-		•	•		
S03e	BATHROOM	-	710	2135	35	A1	HC WOOD	PAINT	-	WOOD	PAINT	-		•	•		
S03f	BATHROOM	-	860	2135	35	C1	HC WOOD	PAINT	-	WOOD	PAINT	-		•			Overhead track detail per manufacturer
S03g	BATHROOM		810	2135	35	C1	HC WOOD	PAINT	-	WOOD	PAINT	-		•			Overhead track detail per manufacturer
S03y		-	1220	2135	45	B1	INSULATED METAL	PAINT	-	METAL	PAINT	METAL		•		•	
S04b	LAUNDRY	-	860	2135	35	A1	HC WOOD	PAINT	-	WOOD	PAINT	-		•			
S04e	LAUNDRY	-	1830	2135	35	B1	HC WOOD	PAINT	-	WOOD	PAINT	-		•			
S04f	LAUNDRY	-	1525	2135	35	B1	HC WOOD	PAINT	-	WOOD	PAINT	-		•			
S04h	LAUNDRY	-	1220	2135	35	B1	HC WOOD	PAINT	-	WOOD	PAINT	-		•			
S05c	CLOSET	-	810	2135	35	A1	HC WOOD	PAINT	-	WOOD	PAINT	-		•			
S05d	CLOSET / HEAT PUMP	-	760	2135	35	A1	HC WOOD	PAINT	-	WOOD	PAINT	-		•			
S05e	CLOSET	-	710	2135	35	A1	HC WOOD	PAINT	-	WOOD	PAINT	-		•			
S05f	CLOSET	-	660	2135	35	A1	HC WOOD	PAINT	-	WOOD	PAINT	-		•			
S05h	CLOSET	-	550	2135	35	A1	HC WOOD	PAINT	-	WOOD	PAINT	-		•			
S05s	CLOSET	-		2135	20	D1	HC WOOD	PAINT	-	WOOD	PAINT	-					Overhead track detail per manufacturer, back-painted glass panels, door width varies

DOOR SCHEDULE - TYPICAL

DOOR NUMBER	TF-From	WALL FIRE RATING	TF-To	FIRE RATING	TEMP. RISE	SIZE WIDTH	SIZE HEIGHT	SIZE THICKNESS	DOOR TYPE	DOOR MATERIAL	DOOR FINISH	DOOR GLAZING	FRAME MATERIAL	FRAME FINISH	FRAME THRESHOLD	HARDWARE POWER OPERATOR	HARDWARE EXIT DEVICE	HARDWARE KICKPLATE	HARDWARE HINGE	HARDWARE LOCK	HARDWARE SELF CLOSER	SECURITY CARD SWIPE	SECURITY ELECTRIC STRIKE	SECURITY MAGLOCK	COMMENTS
T01a		2 HR		1.5 HR		965	2135	35	A2	HC METAL	PAINT	-	METAL	PAINT	-		•								
T02	CORRIDOR	2 HR	GARBAGE CHUTE	1.5 HR	•	965	2135	45	A1	HC METAL	PAINT	-	METAL	PAINT	-			•	•		•				
T03	CORRIDOR	2 HR	ELECTRICAL CLOSET	1.5 HR	•	1525	2135	45	B1	HC METAL	PAINT	-	METAL	PAINT	-				•	•					Flush bolts
T04				1 HR		965	2135	45	A1																

DOOR TYPES

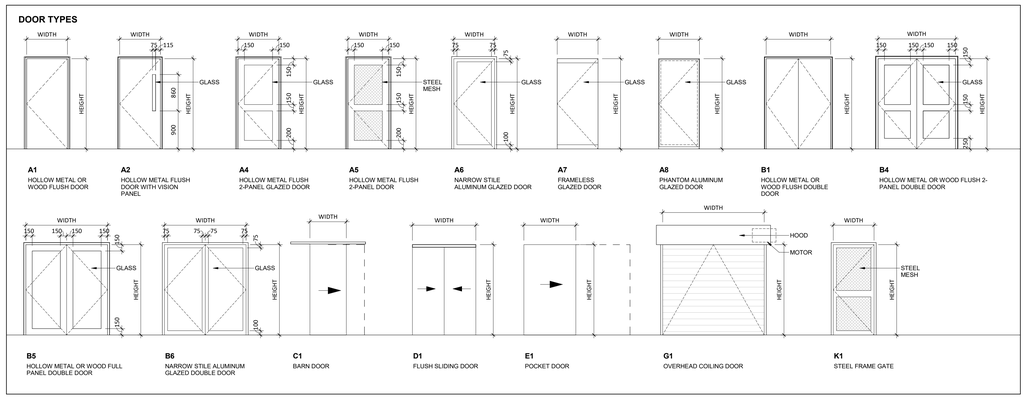

ROOM FINISH SCHEDULE

NUMBER	NAME	FLOOR FINISH	BASE FINISH	WALL FINISH	CEILING FINISH	COMMENTS
P1						
B01-01	PARKING	TRAFFIC COATING	-	PAINT	PAINT	
B01-02	ELEV. LOBBY	-	-	-	-	REFER TO INTERIOR DESIGN DRAWINGS
B01-03	LOCKERS (4)	EPOXY COATING	-	PAINT	PAINT	
B01-03a	ELEV. MACHINE ROOM					
B01-04	VESTIBULE	-	-	-	-	REFER TO INTERIOR DESIGN DRAWINGS
B01-05	LOCKERS (5)	EPOXY COATING	-	PAINT	PAINT	
B01-06	ELECTRICAL ROOM	EPOXY COATING	-	PAINT	PAINT	
B01-07	TELECOM ROOM	EPOXY COATING	-	PAINT	PAINT	
B01-08	WATER METER	EPOXY COATING	-	PAINT	PAINT	
B01-09	VESTIBULE	-	-	-	-	REFER TO INTERIOR DESIGN DRAWINGS
B01-10	VESTIBULE	-	-	-	-	REFER TO INTERIOR DESIGN DRAWINGS
M01-04	LOCKER	EPOXY COATING	-	PAINT	PAINT	
GROUND FLOOR						
F01-01	MAIN VESTIBULE	-	-	-	-	REFER TO INTERIOR DESIGN DRAWINGS
F01-02	LOBBY	-	-	-	-	REFER TO INTERIOR DESIGN DRAWINGS
F01-03	MAIL	-	-	-	-	REFER TO INTERIOR DESIGN DRAWINGS
F01-04	MAIL LOADING	-	-	-	-	REFER TO INTERIOR DESIGN DRAWINGS
F01-05	PARCEL STORAGE	-	-	-	-	REFER TO INTERIOR DESIGN DRAWINGS
F01-06	MOVING ROOM	EPOXY COATING	-	PAINT	PAINT	
F01-07	GARBAGE ROOM	EPOXY COATING	-	PAINT	PAINT	
F01-08	UNIVERSAL WASHROOM	-	-	-	-	REFER TO INTERIOR DESIGN DRAWINGS
F01-09	PET SPA	-	-	-	-	REFER TO INTERIOR DESIGN DRAWINGS
F01-10	VESTIBULE	-	-	-	-	REFER TO INTERIOR DESIGN DRAWINGS
FLOOR 2						
F02-01	FITNESS CENTER	-	-	-	-	REFER TO INTERIOR DESIGN DRAWINGS
F02-02	CLOSET	-	-	-	-	REFER TO INTERIOR DESIGN DRAWINGS
F02-03	YOGA	-	-	-	-	REFER TO INTERIOR DESIGN DRAWINGS
F02-04	CLOSET	-	-	-	-	REFER TO INTERIOR DESIGN DRAWINGS
F02-05	SAUNA	-	-	-	-	REFER TO INTERIOR DESIGN DRAWINGS
F02-06	WOMEN'S WASHROOM	-	-	-	-	REFER TO INTERIOR DESIGN DRAWINGS
F02-07	WOMEN'S CHANGE ROOM	-	-	-	-	REFER TO INTERIOR DESIGN DRAWINGS
F02-08	MEN'S WASHROOM	-	-	-	-	REFER TO INTERIOR DESIGN DRAWINGS
F02-09	MEN'S CHANGE ROOM	-	-	-	-	REFER TO INTERIOR DESIGN DRAWINGS
FLOOR 3						
F03-01	MEMBER'S CLUB	-	-	-	-	REFER TO INTERIOR DESIGN DRAWINGS
F03-02	BARRIER FREE WASHROOM	-	-	-	-	REFER TO INTERIOR DESIGN DRAWINGS
F03-03	WASHROOM	-	-	-	-	REFER TO INTERIOR DESIGN DRAWINGS
F03-04	TV ROOM	-	-	-	-	REFER TO INTERIOR DESIGN DRAWINGS
MPH						
M01-01	MECHANICAL PENTHOUSE	EPOXY COATING	-	PAINT	PAINT	
M01-02	GENERATOR AND COOLER ROOM					

ROOM FINISH SCHEDULE - TYPICAL

NUMBER	NAME	FLOOR FINISH	BASE FINISH	WALL FINISH	CEILING FINISH	COMMENTS
T01-01	CORRIDOR	-	-	-	-	REFER TO INTERIOR DESIGN DRAWINGS
T01-02	STAIR A	-	-	-	-	REFER TO INTERIOR DESIGN DRAWINGS
T01-03	STAIR B	-	-	-	-	REFER TO INTERIOR DESIGN DRAWINGS
T01-04	STAIR C	-	-	-	-	REFER TO INTERIOR DESIGN DRAWINGS
T01-05	GARBAGE	-	-	-	-	REFER TO INTERIOR DESIGN DRAWINGS
T01-06	LOCKER	EPOXY COATING	-	PAINT	PAINT	
T01-07	ELEC. CLOSET	EPOXY COATING	-	PAINT	PAINT	
T01-08	VESTIBULE					

TURNER FLEISCHER

Turner Fleischer Architects Inc.

67 Lesmill Road
Toronto, ON, M3B 2T8
T 416 425 2222
turnerfleischer.com

This drawing, as an instrument of service, is provided by and is the property of Turner Fleischer Architects Inc. and may not be reproduced or distributed in whole or in part without our consent. Contractor on site and must notify Turner Fleischer Architects Inc. of any variations from the supplied information. This drawing is not to be scaled. The architect is not responsible for the accuracy of dimensions and specifications derived from electronic media. Contractor must use and follow all appropriate consultant's drawings before proceeding with the work. Construction must conform to all applicable codes and requirements of authorities having jurisdiction. The contractor working from drawings and specifications issued for construction must assume full responsibility and bear costs for any corrections or damages resulting from his work.

#	DATE	DESCRIPTION	BY
1	2021-12-20	ISSUED FOR BUILDING PERMIT	CJF

TKG TheKawarthaGroup

PROJECT
THE MOORINGS ON CAMERON LAKE
99 LOUISA STREET, FENELON FALLS, ON

DRAWING
DOOR & ROOM FINISH SCHEDULE

PROJECT NO. 21.001CS
PROJECT DATE 2021-05-01
DRAWN BY CJF
CHECKED BY MY
SCALE 1 : 50

DRAWING NO. A701
REV. 1

2022-02-22 12:27:54 PM