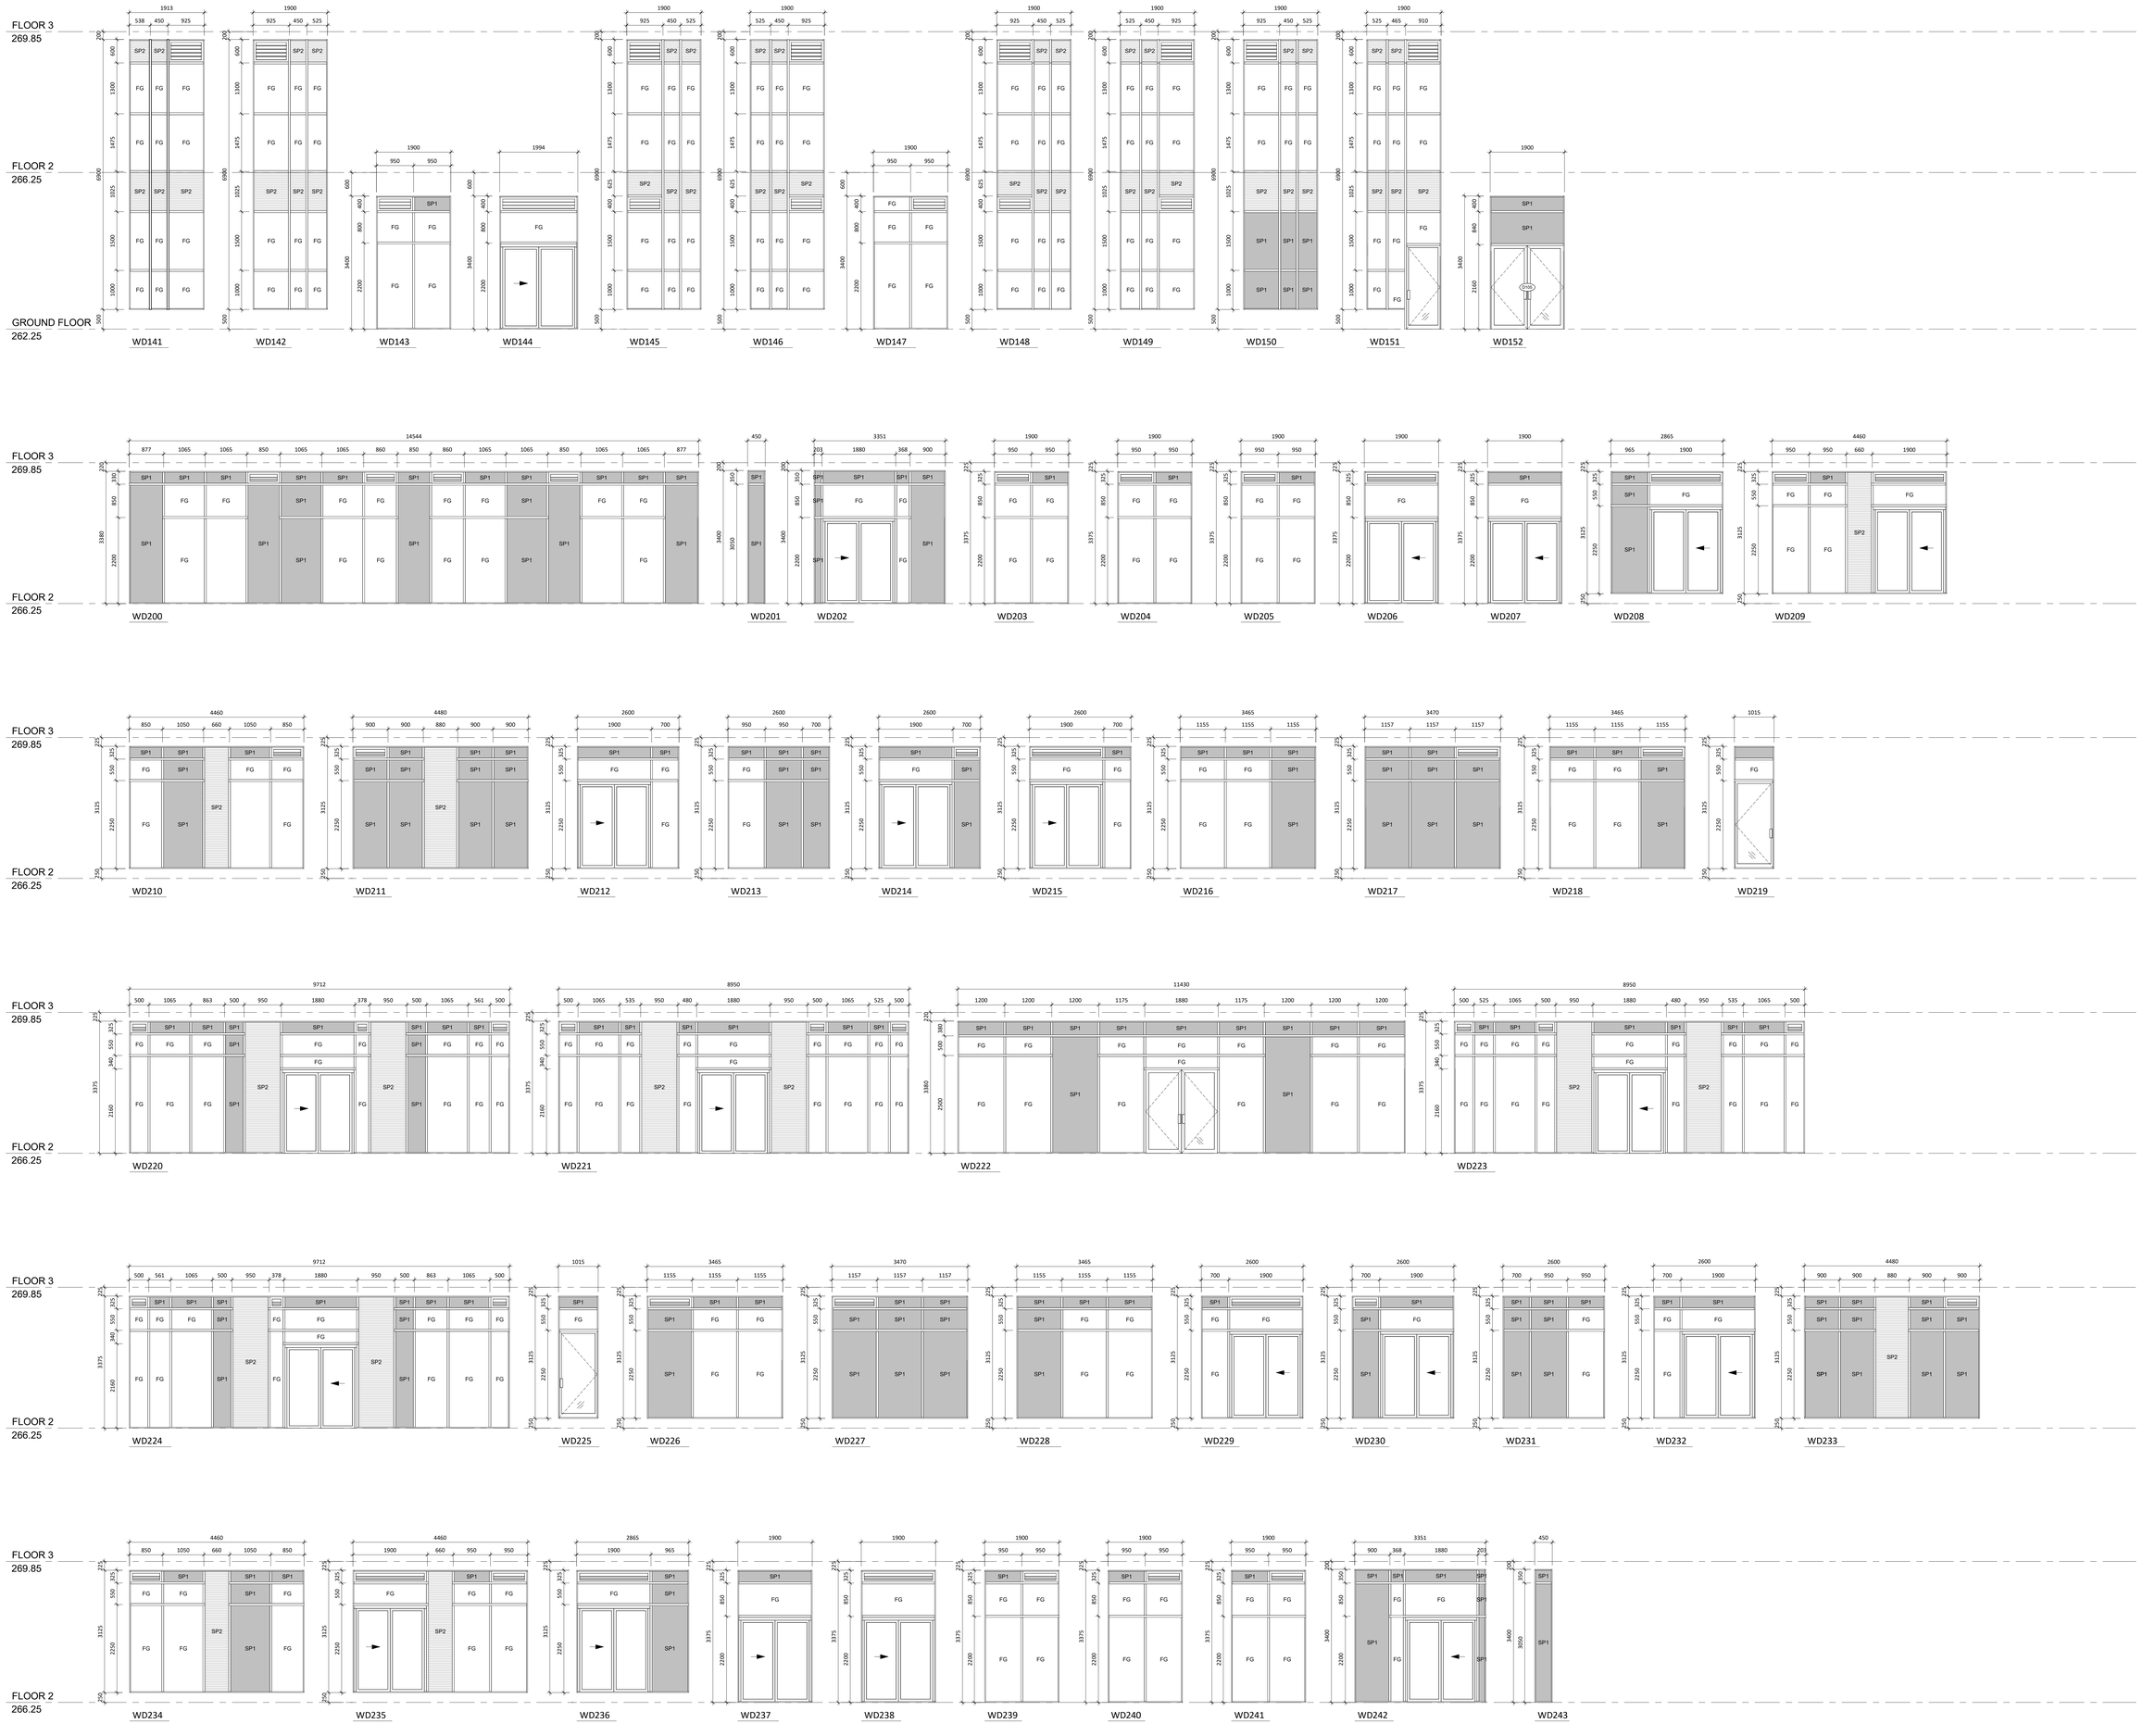

TURNER FLEISCHER

Turner Fleischer Architects Inc.

67 Lesmill Road
Toronto, ON, M3B 2T8
T 416 425 2222
turnerfleischer.com

This drawing, as an instrument of service, is provided by and is the property of Turner Fleischer Architects Inc. and may not be reproduced or distributed in whole or in part without our consent. Contractor shall verify and take responsibility for all dimensions and conditions on site and must notify Turner Fleischer Architects Inc. of any variations from the supplied information. This drawing is not to be scaled. The architect is not responsible for the accuracy of CAD files prepared by other consultants. Contractor shall determine and verify all as built CAD files from appropriate consultant's drawings before proceeding with the work. Construction must conform to all applicable codes and requirements of authorities having jurisdiction. The contractor working from drawings and specifications issued for construction must assume full responsibility and bear costs for any corrections or damages resulting from his work.

FG INSULATING UNIT (CLEAR)

GL2 INSULATING UNIT (TINTED)

SP1 SPANDREL GLASS UNIT - COLOUR (TBD)

SP2 SPANDREL GLASS UNIT - COLOUR (TBD)

LV1 ALUMINUM WALL LOUVER - COLOUR (TBD)

AP1 ALUMINUM SHEET PANEL - COLOUR (TBD)

WINDOW DESIGNATION

WW0-00

- WINDOW NUMBER
- 00 - FLOOR NUMBER
  - T - TYPICAL FLOOR (X-X)
  - MP - MECHANICAL PENTHOUSE
- 00 - FLOOR NUMBER
  - T - TYPICAL FLOOR (X-X)
  - MP - MECHANICAL PENTHOUSE

GENERAL NOTES - WINDOWS:

1. COMPLY WITH PRODEMITY REQUIRENMENTS FOR WINDOW WALL SYSTEMS.
2. UNLESS OTHERWISE NOTED, ALL DOOR AND WINDOWS SHALL BE DOUBLE GLAZED SEALED UNITS ON PREFINISHED ALUM. FRAMING SYSTEM
3. WINDOW CONTRACTOR TO COORDINATE WITH MECHANICAL & ELECTRICAL TRADES FOR POSSIBLE EXHAUST/SUPPLY AIR GRILLES PENETRATIONS THRU WINDOWS
4. WINDOW SIZE AS SHOWN ARE SUBJECT TO CHANGES AND TO BE USED FOR PRICING PURPOSES ONLY, FINAL SIZING, COORDINATE WITH ARCHITECT PRIOR TO FABRICATION
5. REFER TO GENERAL NOTES ON DRAWING A004 FOR WINDOWS AND GUARDS
6. REFER TO INTERIOR DESIGN DRAWIINGS FOR ALL INTERIOR ALUMINUM SCREENS/GLAZING
7. WINDOW SUPPLIER TO PROVIDE INSULATED METAL PANEL CORNERS AND INFILLS,FINISH TO MATCH FRAMES.
8. WINDOW SUPPLIER TO PROVIDE JAM CLOSURES.

#	DATE	DESCRIPTION	BY

TKG TheKawarthaGroup

PROJECT

THE MOORINGS ON CAMERON LAKE

99 LOUISA STREET, FENELON FALLS, ON

DRAWING

WINDOW SCHEDULE - GROUND AND SECOND

PROJECT NO.	21.001CS
PROJECT DATE	2021-05-01
DRAWN BY	CJF
CHECKED BY	MY
SCALE	1 : 50
DRAWING NO.	A712
REV.	

2022-02-22 12:28:16 PM